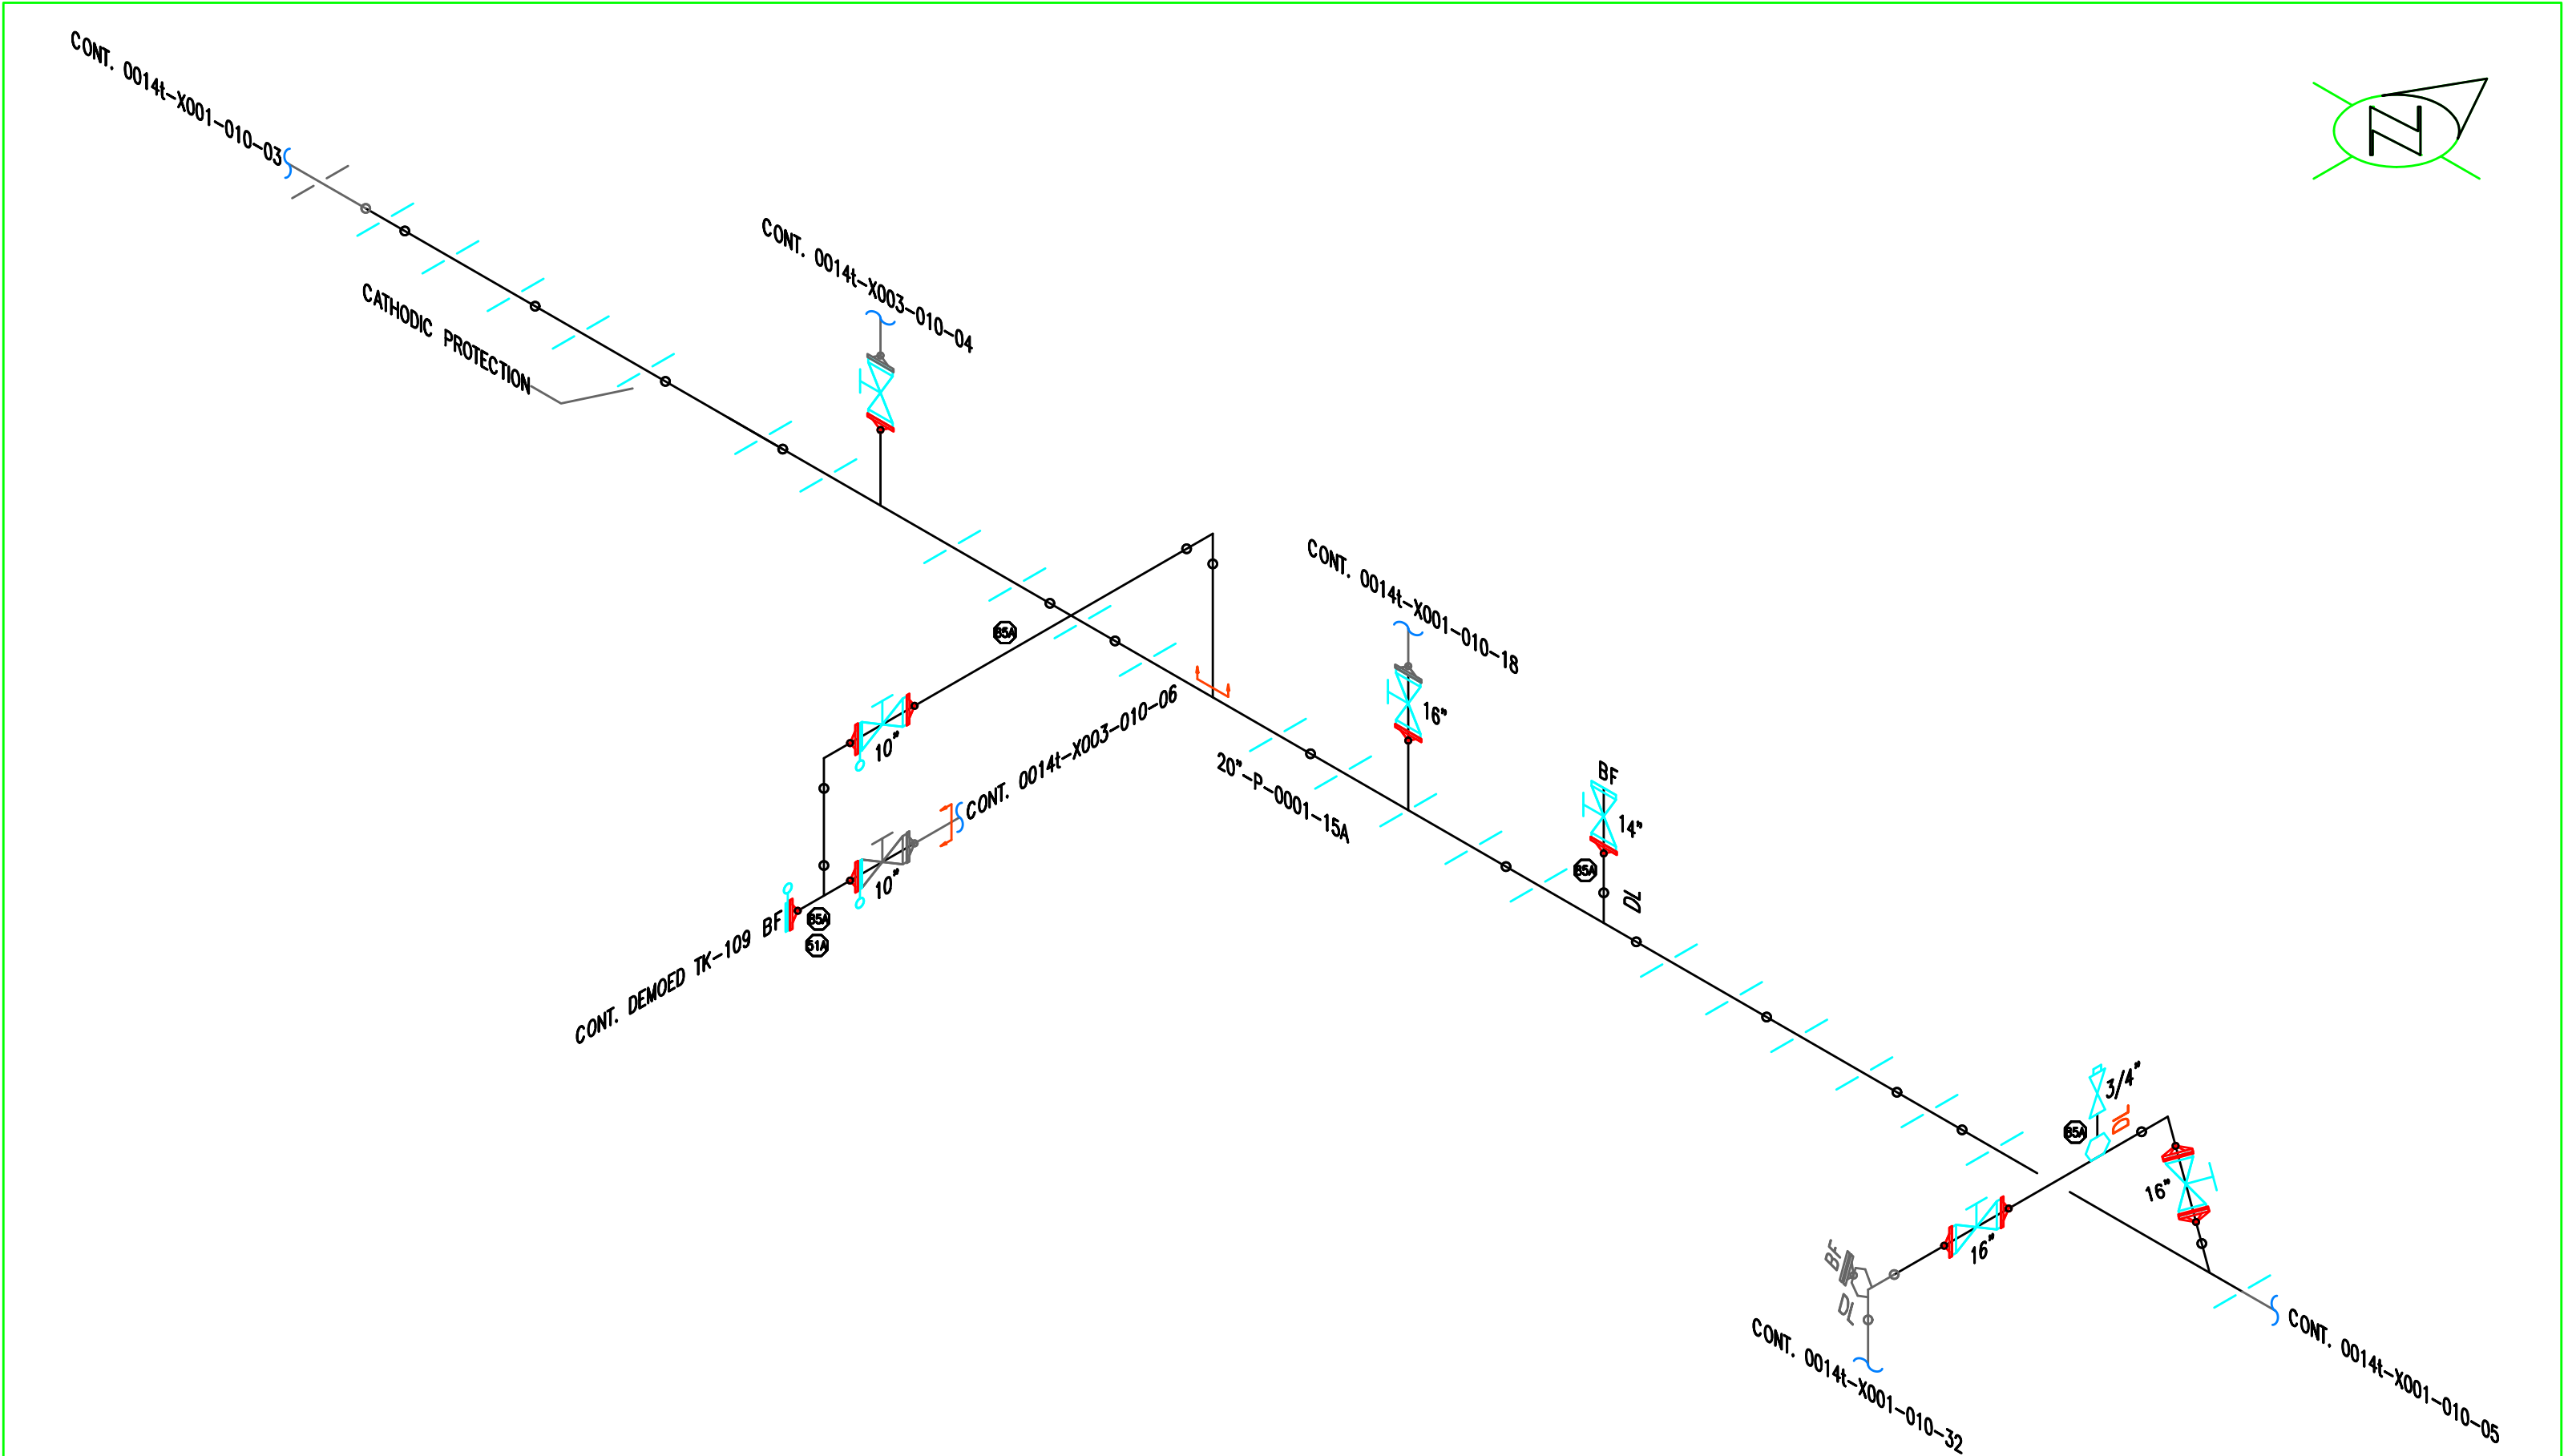


REFERENCES		CML LEGEND		NOTES		ISSUED FOR FEAS PROJECT		 Chevron Pasadena Refinery		MATERIAL		INSPECTION PIPING ISOMETRIC											
P&ID	LEGACY ISO	☐ 0" SHOT	1. API PIPE CLASS -	☐ 0" AND 90° SHOT	2. CVX PIPE SPEC -																		
14A-11-F14801	14-CRUDE-L001 PG. 2 OF 16	☐ SINGLE POINT UT	3. OP TEMP. -			05/19/25																	
		☐ 4 POINT UT	4. FROM -																				
		☐ SCAN UT (100%)	5. TO -																				
		☐ GRID UT	6. MISC. -																				
		☐ AUTOMATED UT																					
		+ ADDITIONAL INSPECTION CML	* SULFIDATION POINT									PLANT NUMBER	SYSTEM NUMBER	CIRCUIT NUMBER	SHEET NUMBER	REV.							
								DR. BY:	PART	DATE:	05/19/25	INSULATED?	NO		0014t	-	X001	-	010	-	04		0
								CHK. BY:	PART	DATE:	-	PWHT?	NO										