
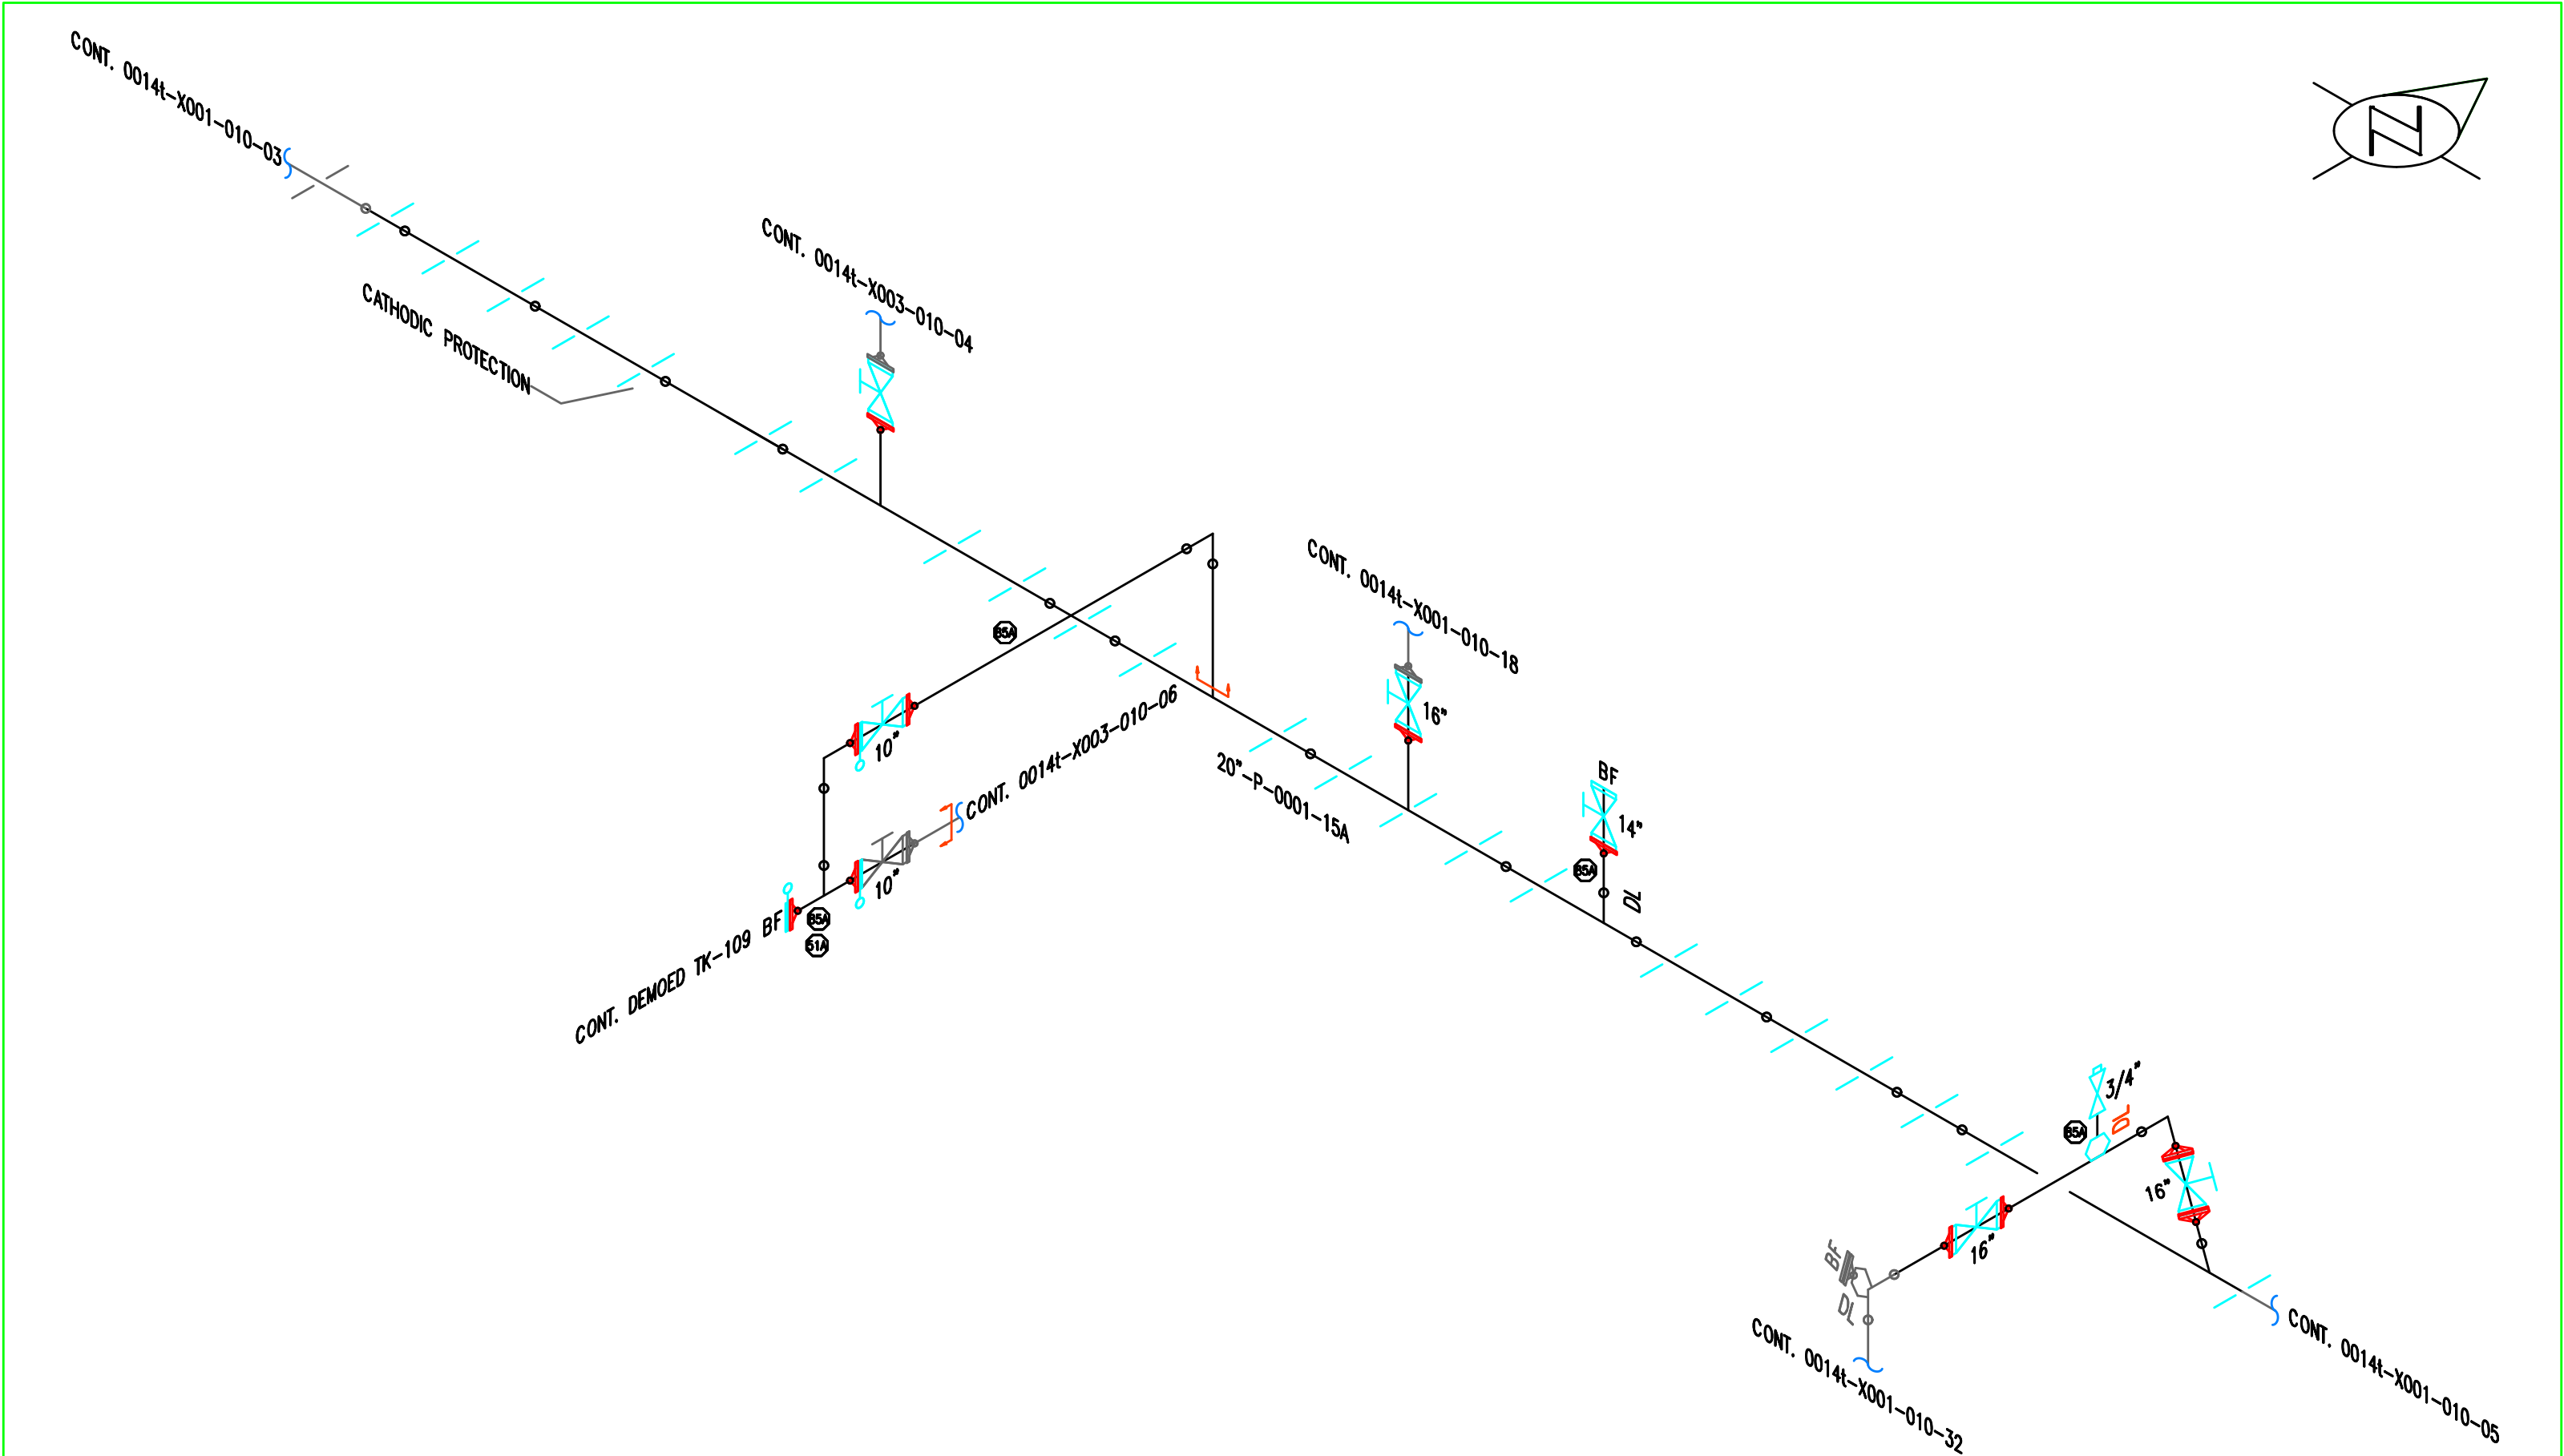


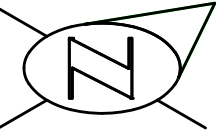

REFERENCES		CML LEGEND		NOTES		ISSUED FOR FEAS PROJECT		Chevron Pasadena Refinery		MATERIAL		INSPECTION PIPING ISOMETRIC					
P&ID	LEGACY ISO																
14A-11-F14801	14-CRUDE-L001 PG. 2 OF 15	RT1 0° SHOT		1. API PIPE CLASS -	REVISIONS	05/19/25											
-	-	RT2 0° AND 90° SHOT		2. CVX PIPE SPEC -													
-	-	UT1 SINGLE POINT UT		3. OP TEMP. -													
-	-	UT4 4 POINT UT		4. FROM -													
-	-	UT8 SCAN UT (100%)		5. TO -													
-	-	UT6 GRID UT		6. MISC. -													
-	-	AUT AUTOMATED UT															
-	-	+ ADDITIONAL INSPECTION CML		* SULFIDATION POINT													