
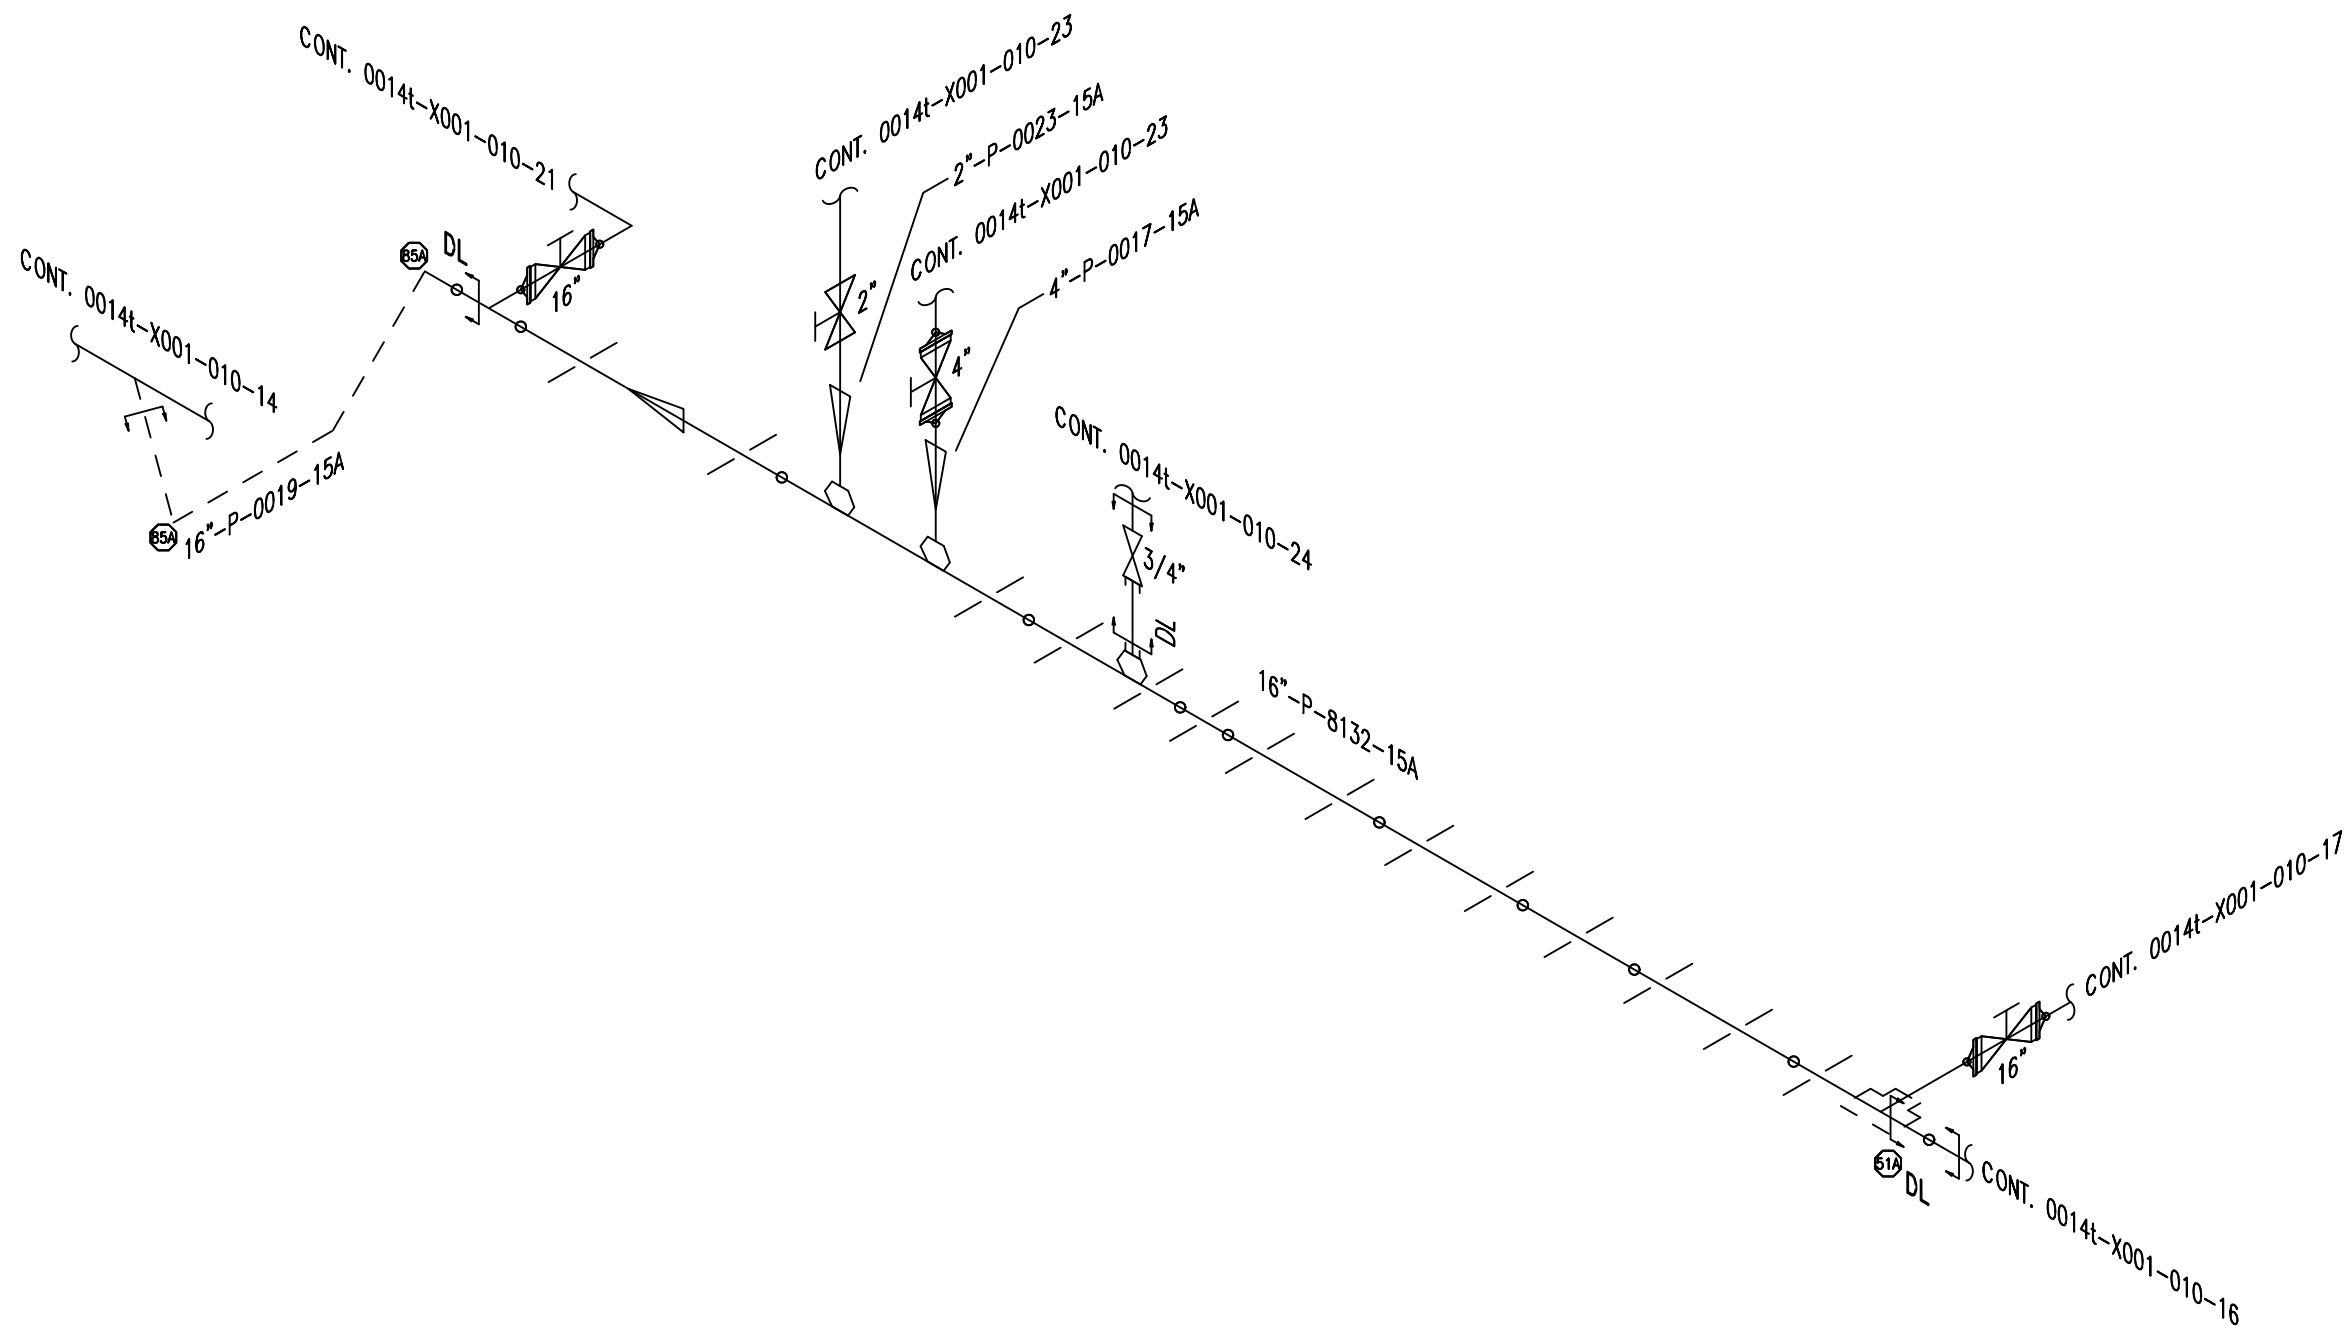


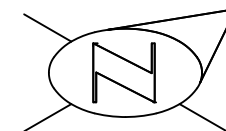

REFERENCES		CML LEGEND		NOTES		ISSUED FOR FEAS PROJECT 05/20/25		 Chevron Pasadena Refinery		MATERIAL		INSPECTION PIPING ISOMETRIC					
P&ID	LEGACY ISO																
14t-11-F14501	14-CRUDE-L001 PG. 11 OF 15	RT1	0° SHOT	1. API PIPE CLASS -	REVISIONS	△				-							
-	14-CRUDE-L003 PG. 12 OF 14	RT2	0° AND 90° SHOT	2. CVX PIPE SPEC -						-							
-	14-CRUDE-L004 PG. 8 OF 10	UT1	SINGLE POINT UT	3. OP TEMP. -						-							
-	-	UT4	4 POINT UT	4. FROM -						-							
-	-	UT8	SCAN UT (100%)	5. TO -						-							
-	-	UT9	GRID UT	6. MISC. -						-							
-	-	AUT	AUTOMATED UT							-							
-	-	+ ADDITIONAL INSPECTION CML		✱ SULFIDATION POINT		DR. BY:	PART	DATE:	05/20/25	INSULATED?	NO	PLANT NUMBER	SYSTEM NUMBER	CIRCUIT NUMBER	SHEET NUMBER	REV.	
-	-					CHK. BY:	PART	DATE:	-	PWHT?	NO	0014t - X001 - 010 - 15					0