Evaluation only.
Created with Aspose.CAD.
Copyright 2016-2026 Aspose Pty Ltd.

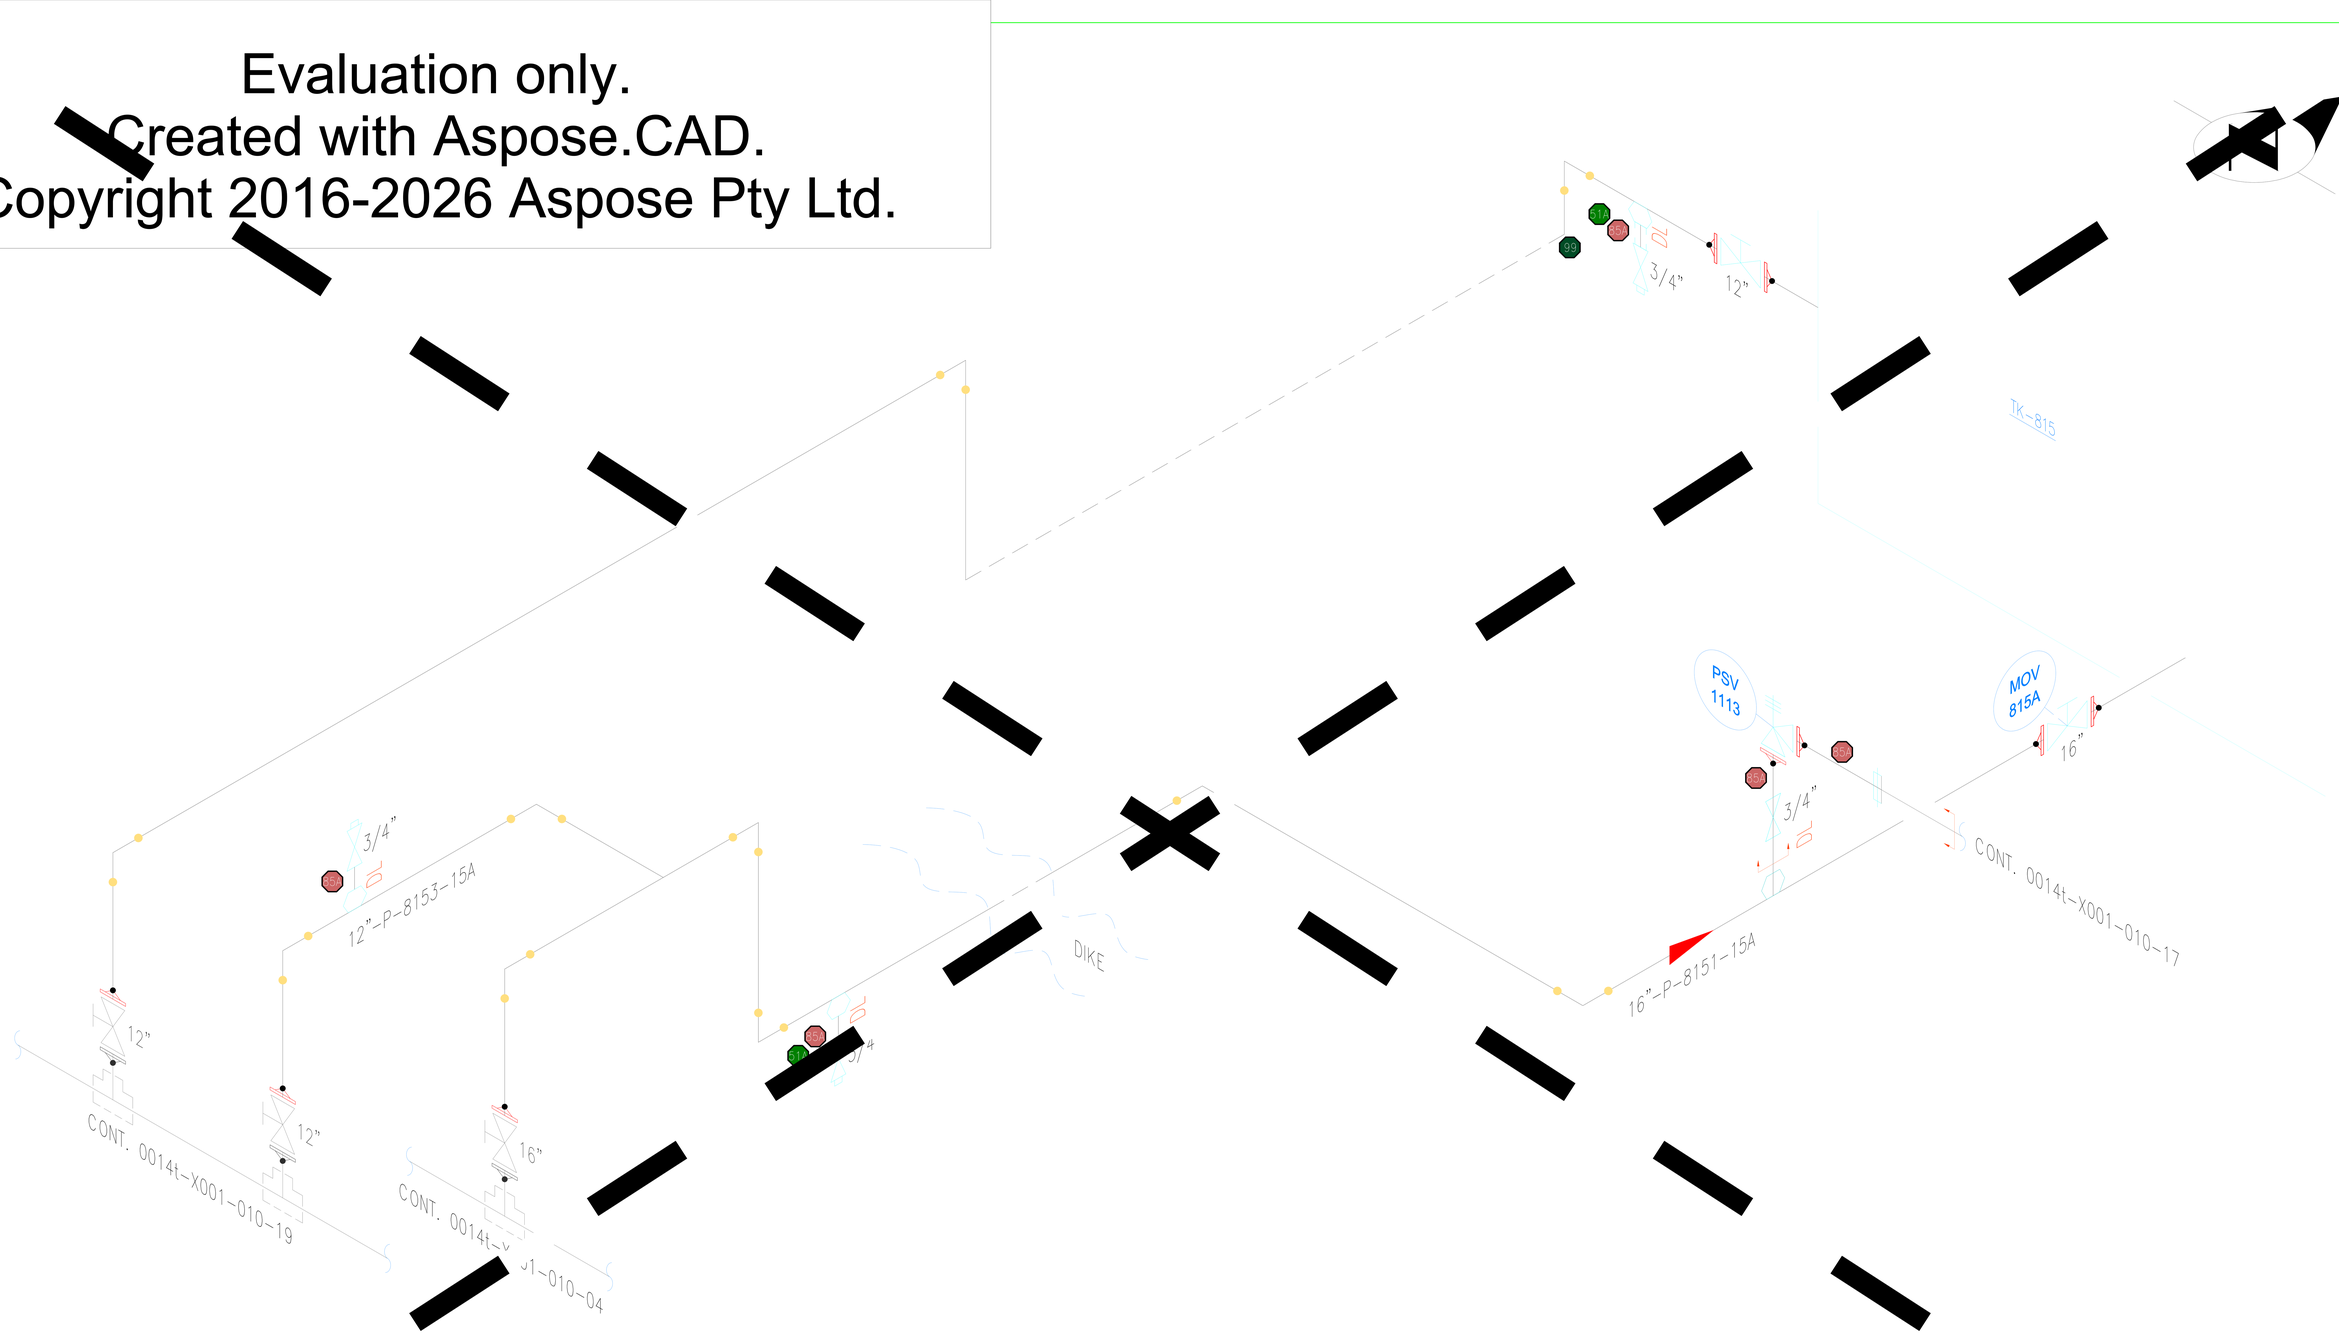

REFERENCES	
P&ID	LEGAC
14t-11-F14501	14-CRUDE-L001 PG. 2 OF 15
-	14-CRUDE-L001 PG. 11 OF 15
-	14-CRUDE-L002 PG. 9 OF 13
-	14-CRUDE-L004 PG. 9 OF 10
-	-
-	-

CML LEGEND	
RT1	0° SHOT
RT2	0° AND 90° SHOT
UT1	SINGLE POINT UT
UT4	4 POINT UT
UTS	SCAN UT (100%)
UTG	GRID UT
AUT	AUTOMATED UT
+	ADDITIONAL INSPECTION CML

NOTES

1. API PIPE CLASS -
2. CVX PIPE SPEC -
3. OP TEMP. -
4. FROM -
5. TO -
6. MISC. -

✱ SULFIDATION POINT

REVISIONS

0	ISSUED FOR FEAS PROJECT	05/23/25

Chevron
Pasadena Refinery

DR. BY:	PART	DATE:	05/23/25
CHK. BY:	PART	DATE:	-

MATERIAL

-
-
-
-
-

INSULATED? NO
PWHT? NO

INSPECTION PIPING ISOME[illegible]

-
-
-

PLANT NUMBER	SYSTEM NUMBER	CIRCUIT NUMBER	SHEET N[illegible]	[illegible]R	REV.
0014t	X001	010	18		0