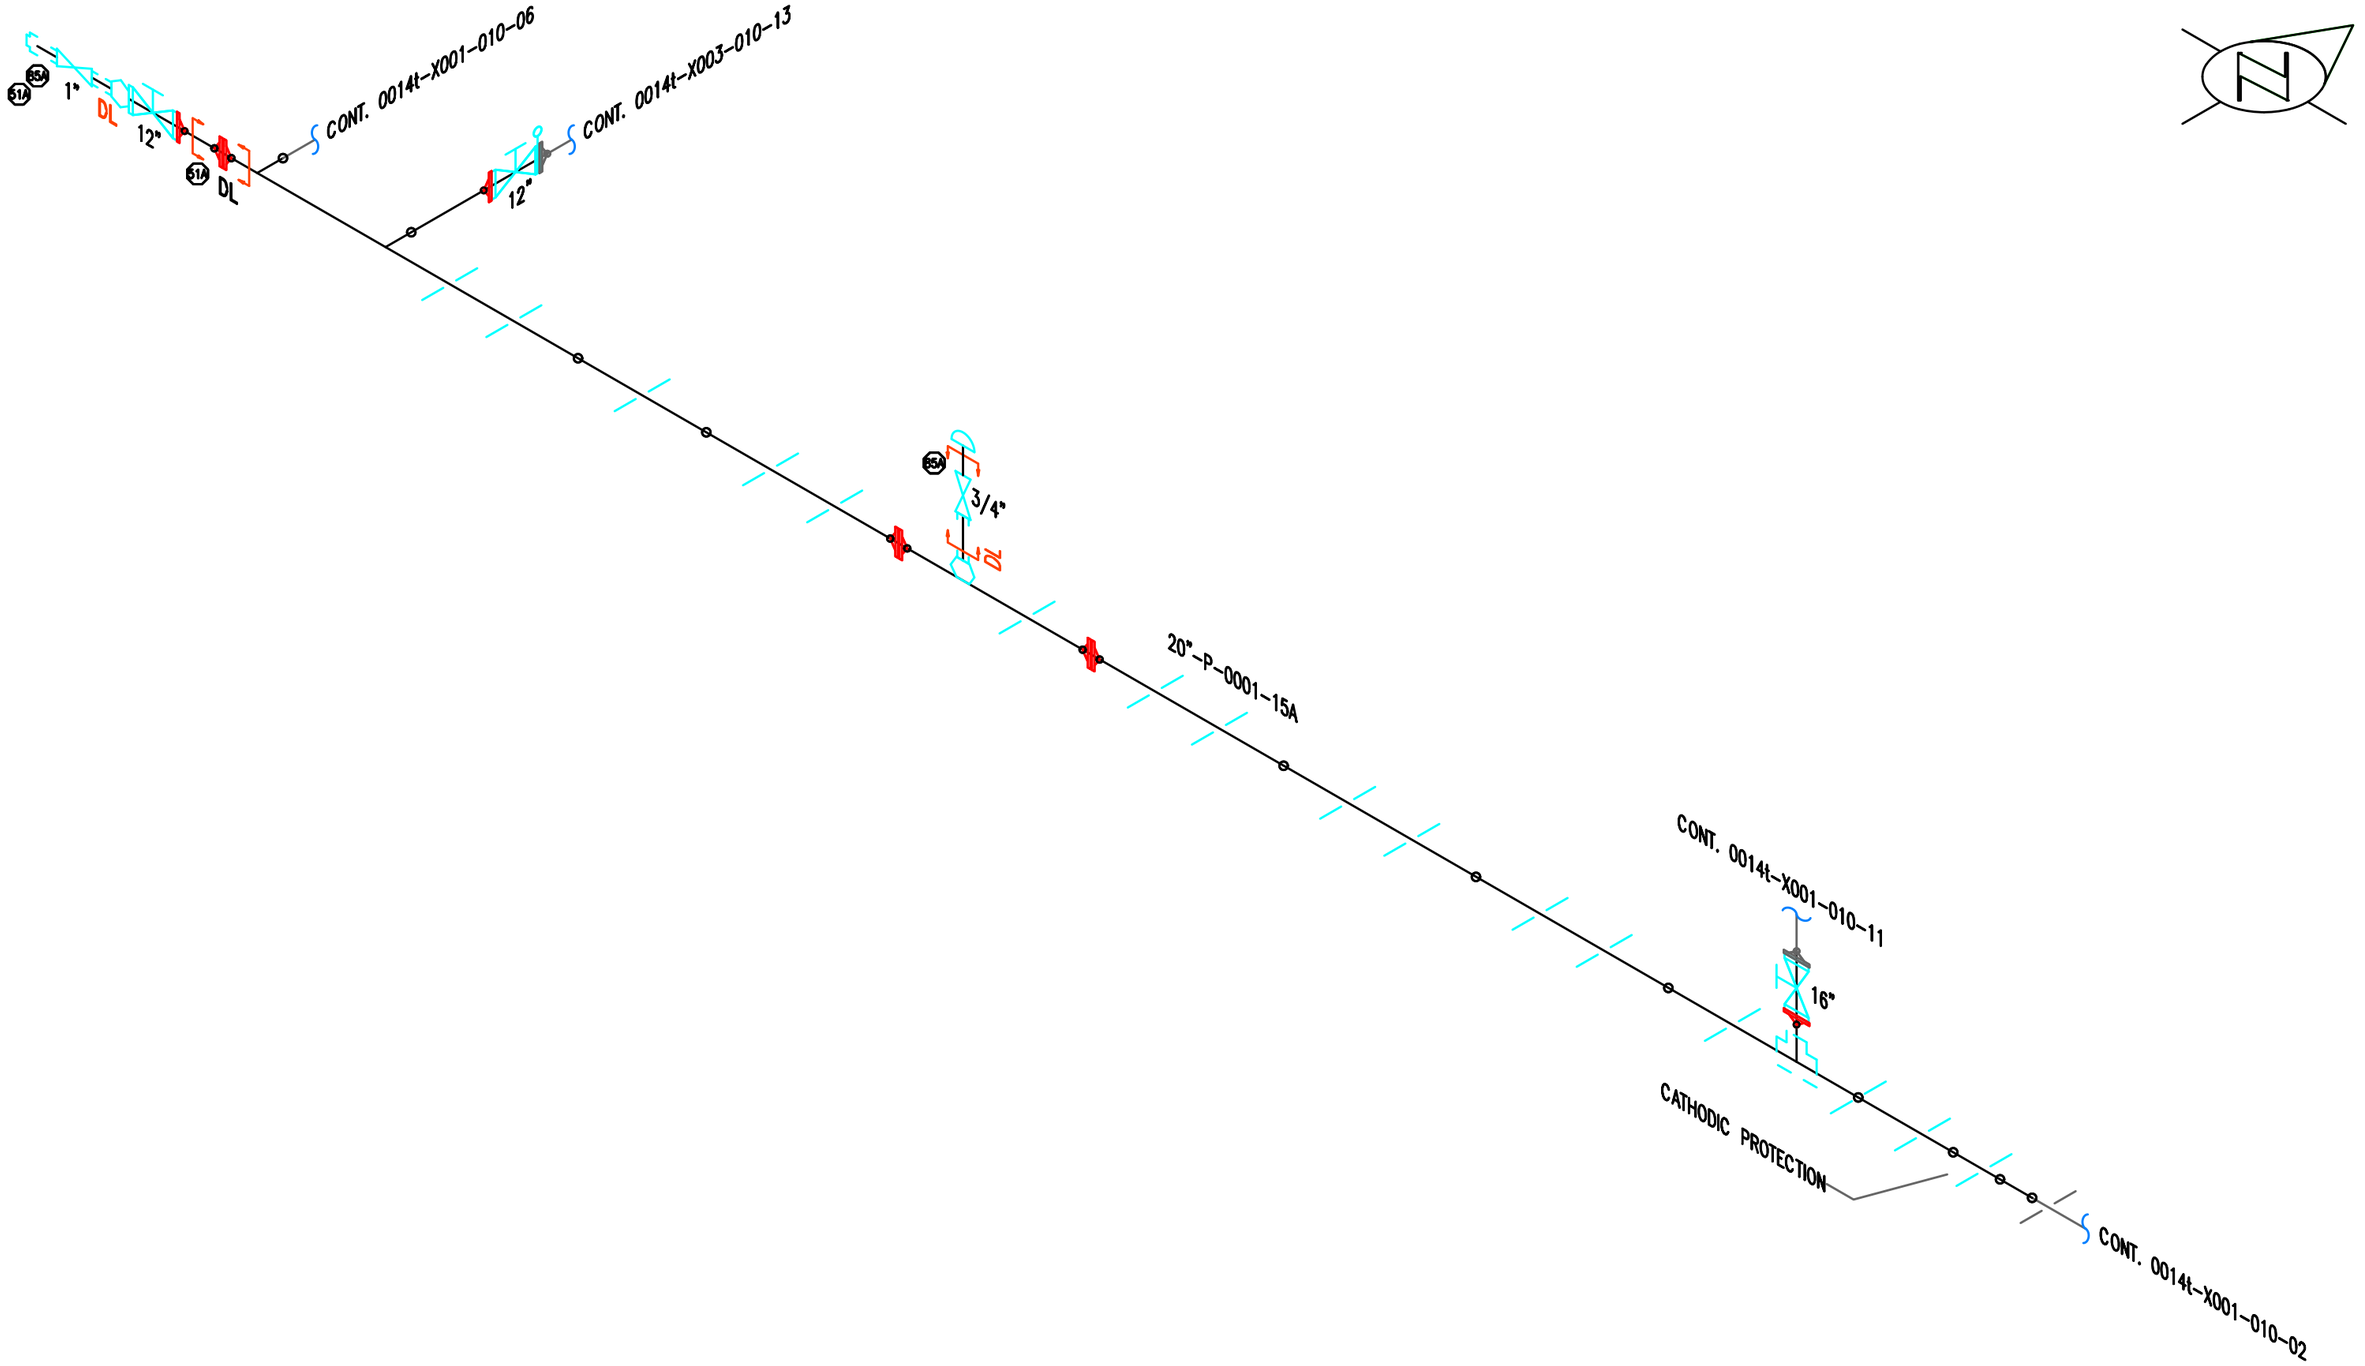


REFERENCES	
P&ID	LEGACY ISO
14T-11-F14600	14-CRUDE-L001 PG. 1 OF 15
-	14-CRUDE-L001 PG. 5 OF 15
-	-
-	-
-	-
-	-

CML LEGEND	
RT1	0° SHOT
RT2	0° AND 90° SHOT
UT1	SINGLE POINT UT
UT4	4 POINT UT
UTS	SCAN UT (100%)
UTG	GRID UT
AUT	AUTOMATED UT
+	ADDITIONAL INSPECTION CML

NOTES
1. API PIPE CLASS -
2. CVX PIPE SPEC -
3. OP TEMP. -
4. FROM -
5. TO -
6. MISC. -
✲ SULFIDATION POINT

REVISIONS

0	ISSUED FOR FEAS PROJECT	05/16/25
△		

Chevron
Pasadena Refinery

DR. BY:	PART	DATE:	05/16/25	-
CHK. BY:	PART	DATE:	-	

MATERIAL	
-	
-	
-	
-	
-	
INSULATED?	NO
PWHT?	NO

INSPECTION PIPING ISOMETRIC

-
-
-

PLANT NUMBER	SYSTEM NUMBER	CIRCUIT NUMBER	SHEET NUMBER	REV.
0014t -	X001 -	010 -	01	0