
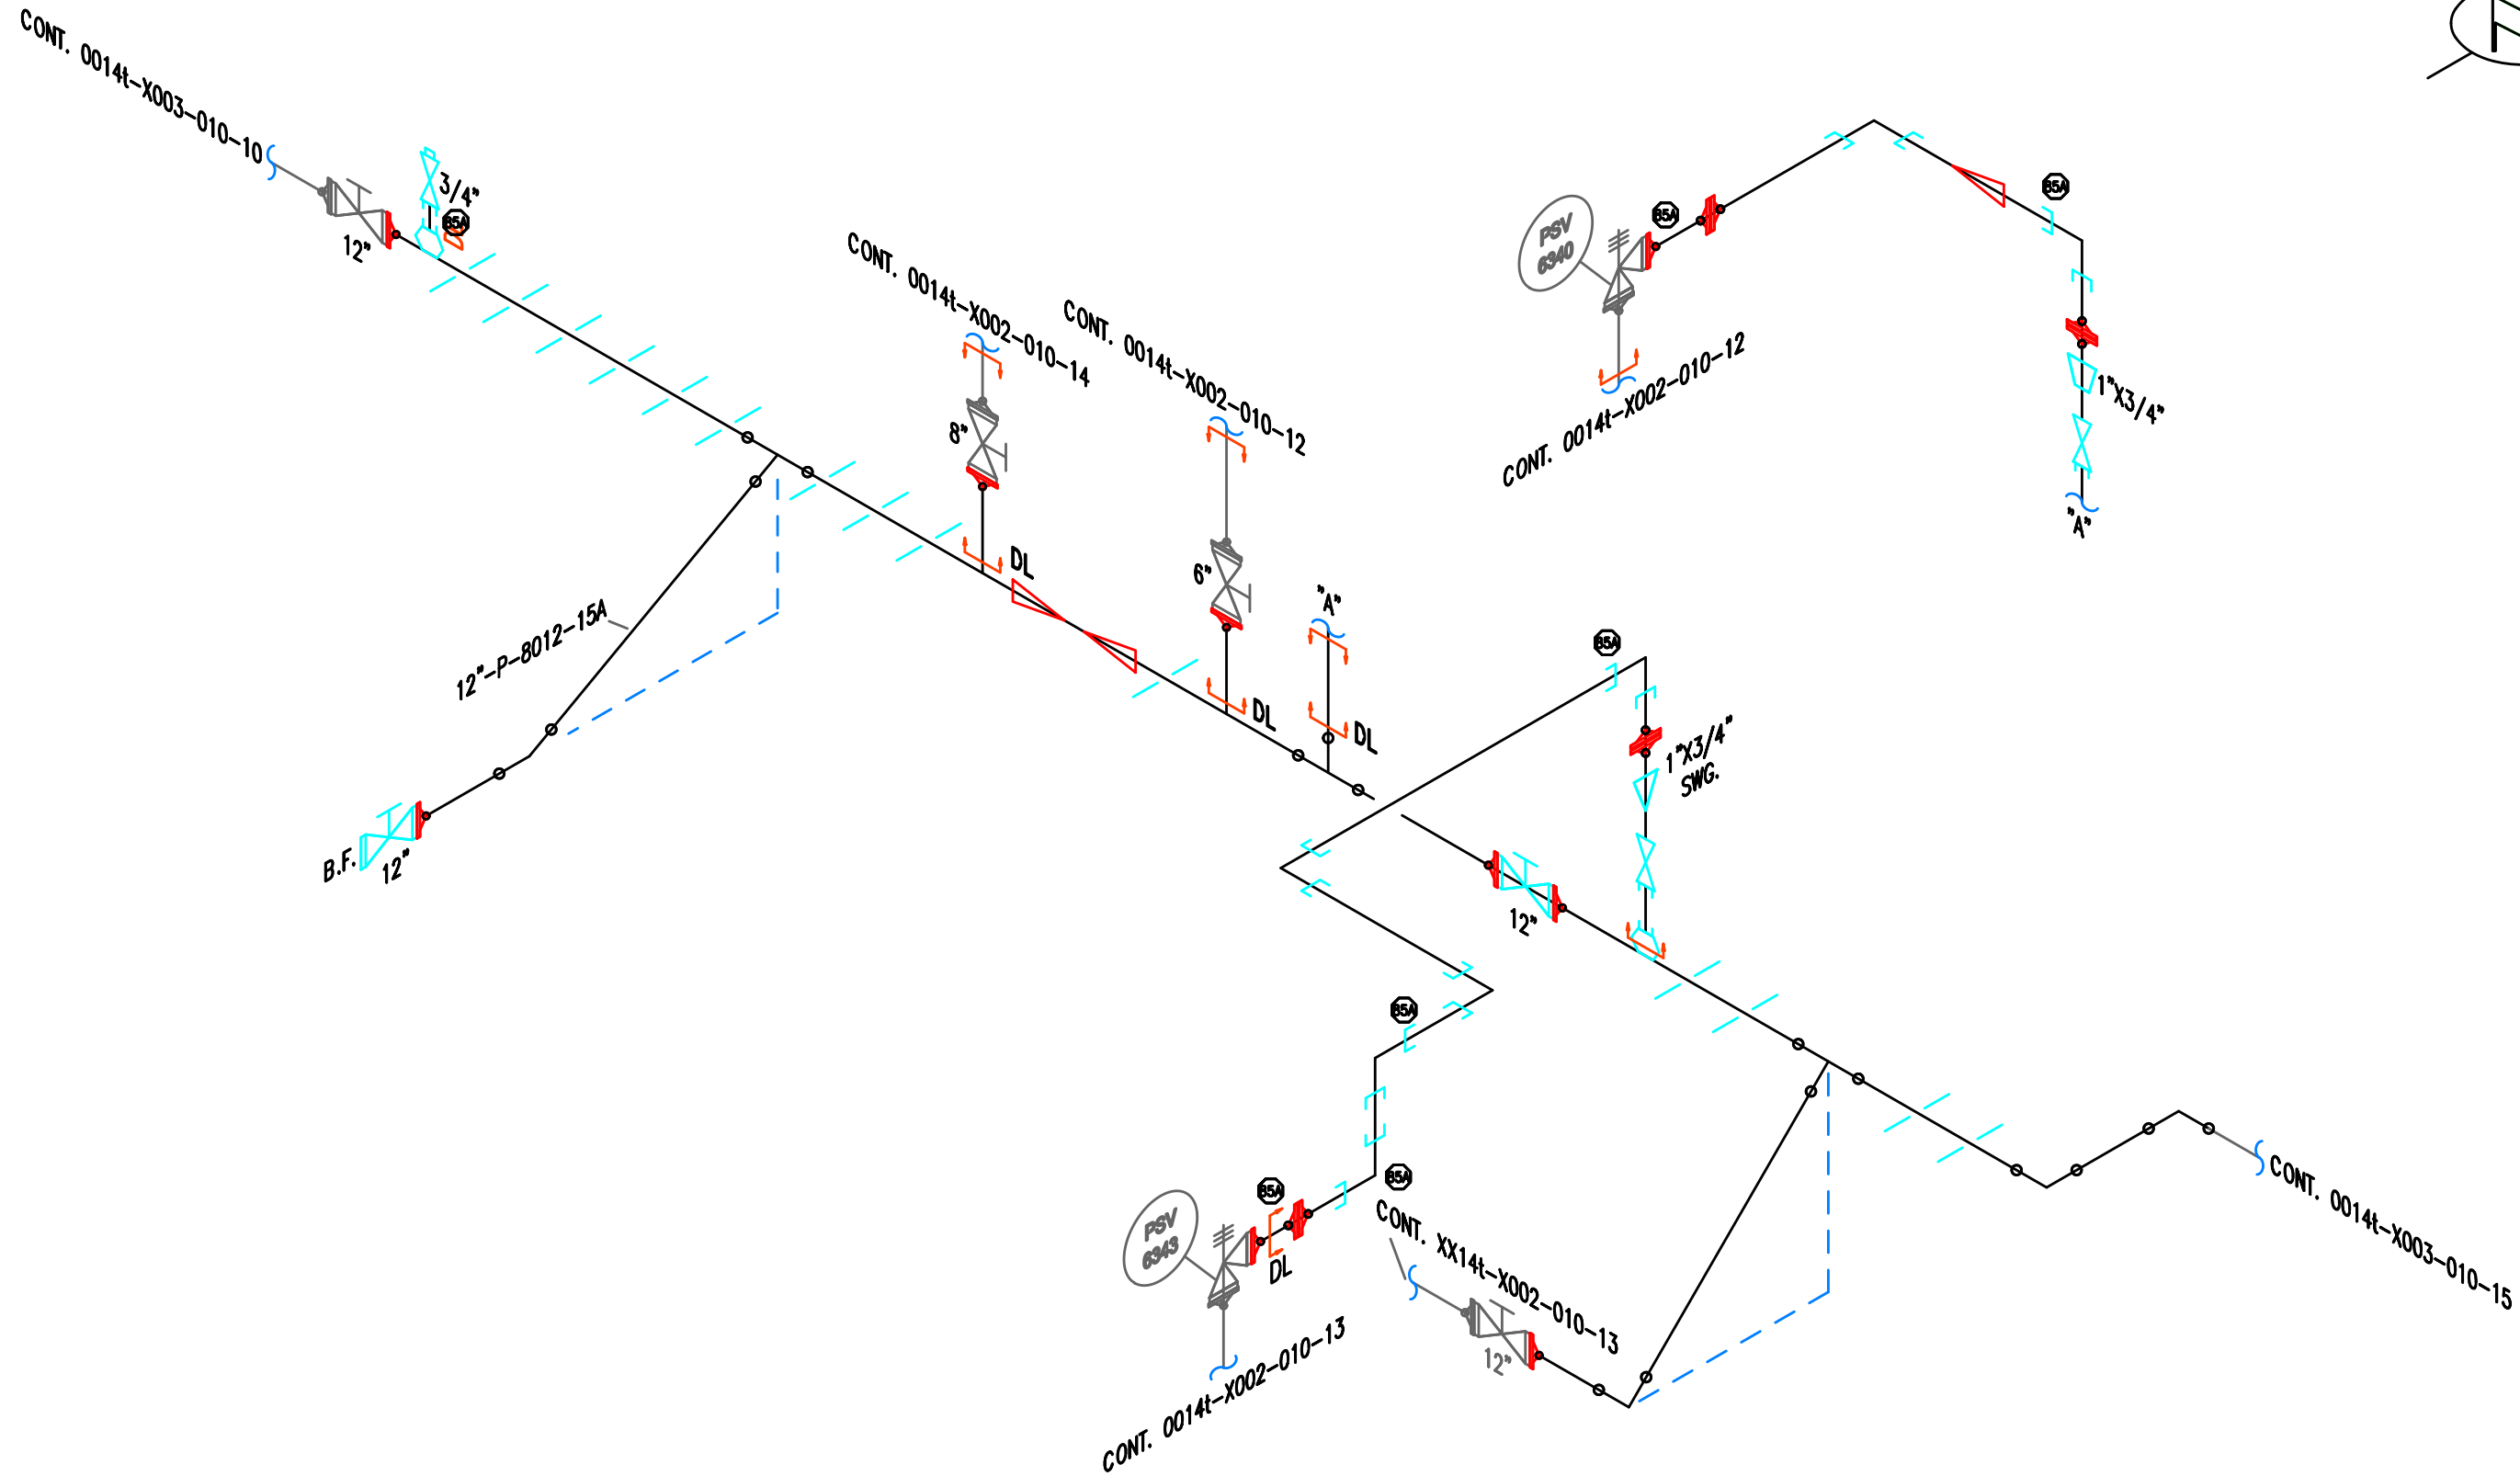


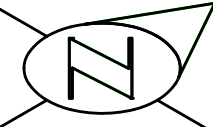

REFERENCES		CML LEGEND		NOTES		ISSUED FOR FEAS PROJECT		 Chevron Pasadena Refinery		MATERIAL		INSPECTION PIPING ISOMETRIC				
P&ID	LEGACY ISO	RT1	0° SHOT	1. API PIPE CLASS -	05/20/25											
14A-11-F14800	14-CRUDE-L003 PG. 8 OF 14	RT2	0° AND 90° SHOT	2. CVX PIPE SPEC -	REVISIONS	△										
-	14-CRUDE-L003 PG. 9 OF 14	UT1	SINGLE POINT UT	3. OP TEMP. -												
-	14-CRUDE-L004 PG. 4 OF 10	UT4	4 POINT UT	4. FROM -												
-	14-CRUDE-L004 PG. 5 OF 10	UT8	SCAN UT (100%)	5. TO -												
-	14-CRUDE-L004 PG. 6 OF 10	UT6	GRID UT	6. MISC. -												
-	14-CRUDE-L004 PG. 6 OF 10	AUT	AUTOMATED UT	* SULFIDATION POINT												
-	-	+	ADDITIONAL INSPECTION CML													
						DR. BY:	PART	DATE:	05/20/25	INSULATED?	NO	PLANT NUMBER				
						CHK. BY:	PART	DATE:	-	PWHT?	NO	SYSTEM NUMBER				
												CIRCUIT NUMBER				
												SHEET NUMBER				
												REV.				
												0014t - X003 - 010 - 14				
												0				