
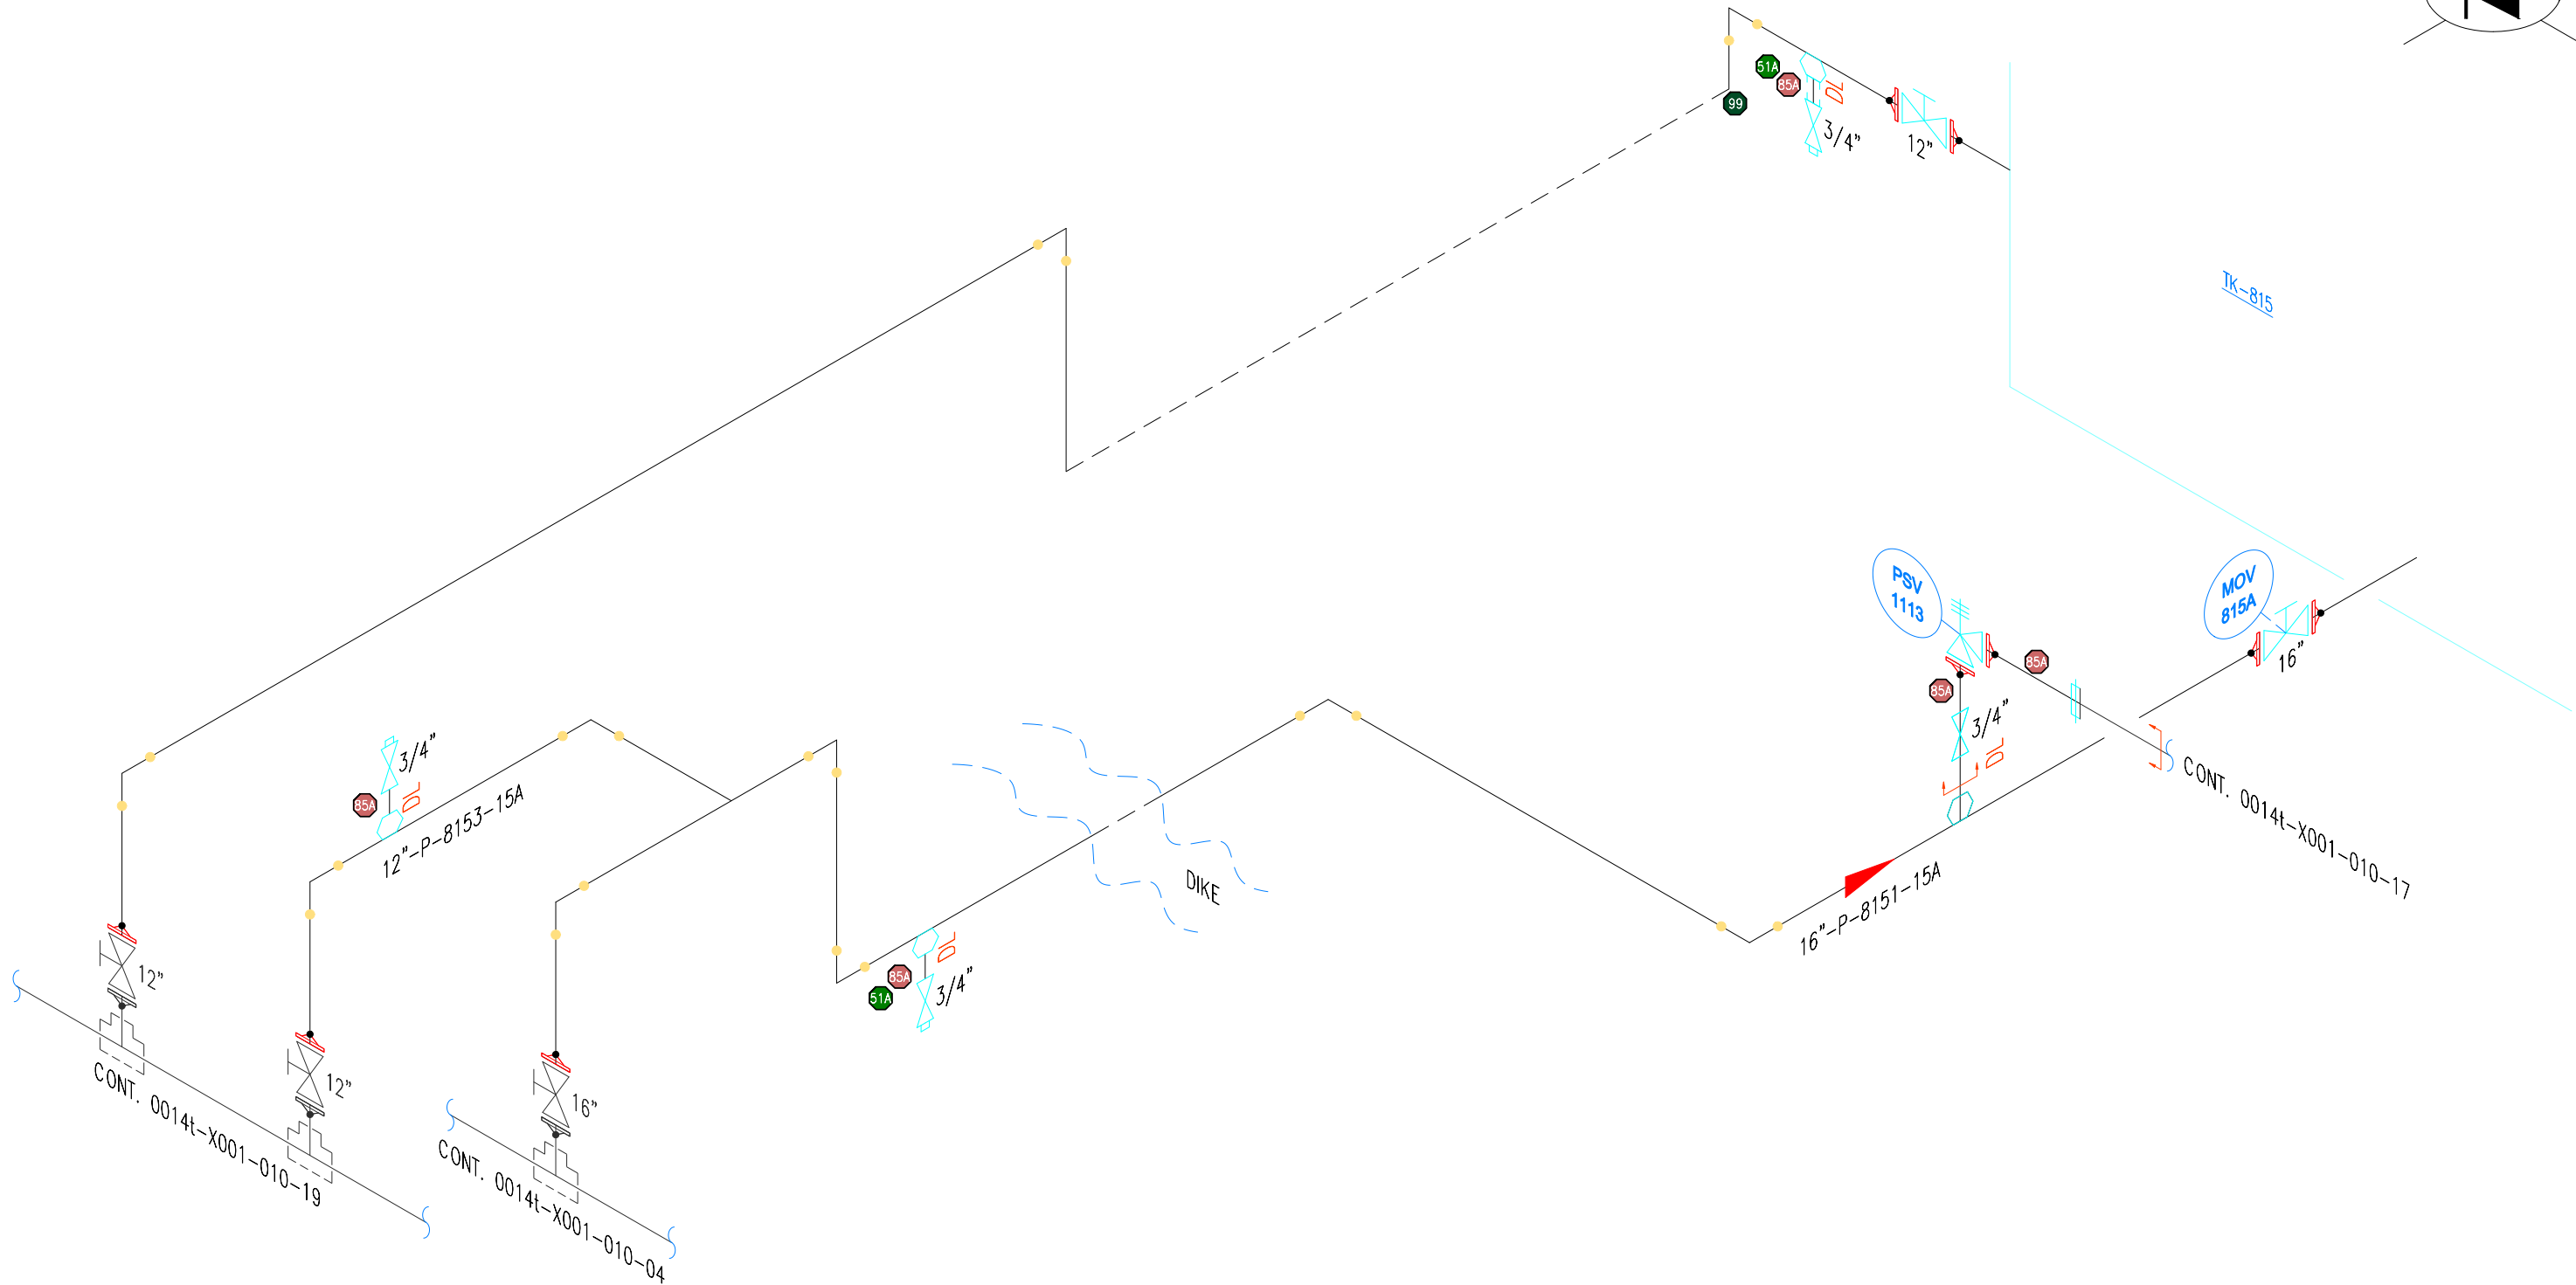


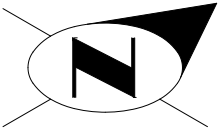

REFERENCES		CML LEGEND	NOTES	ISSUED FOR FEAS PROJECT		MATERIAL		INSPECTION PIPING ISOMETRIC				
P&ID	LEGACY ISO											
14t-11-F14501	14-CRUDE-L001 PG. 2 OF 15	☐ RT1 0° SHOT	1. API PIPE CLASS -	REVISIONS	05/23/25	 Chevron Pasadena Refinery	-	-				
-	14-CRUDE-L001 PG. 11 OF 15	☐ RT2 0° AND 90° SHOT	2. CVX PIPE SPEC -					-				
-	14-CRUDE-L002 PG. 9 OF 13	☐ UT1 SINGLE POINT UT	3. OP TEMP. -					-				
-	14-CRUDE-L004 PG. 9 OF 10	☐ UT4 4 POINT UT	4. FROM -					-				
-	-	☐ UTS SCAN UT (100%)	5. TO -					-				
-	-	☐ UTG GRID UT	6. MISC. -				INSULATED? NO	PLANT NUMBER SYSTEM NUMBER CIRCUIT NUMBER SHEET NUMBER REV.				
-	-	☐ AUT AUTOMATED UT	* SULFIDATION POINT					0014t - X001 - 010 - 18 0				
-	-	+ ADDITIONAL INSPECTION CML					PWHT? NO					