
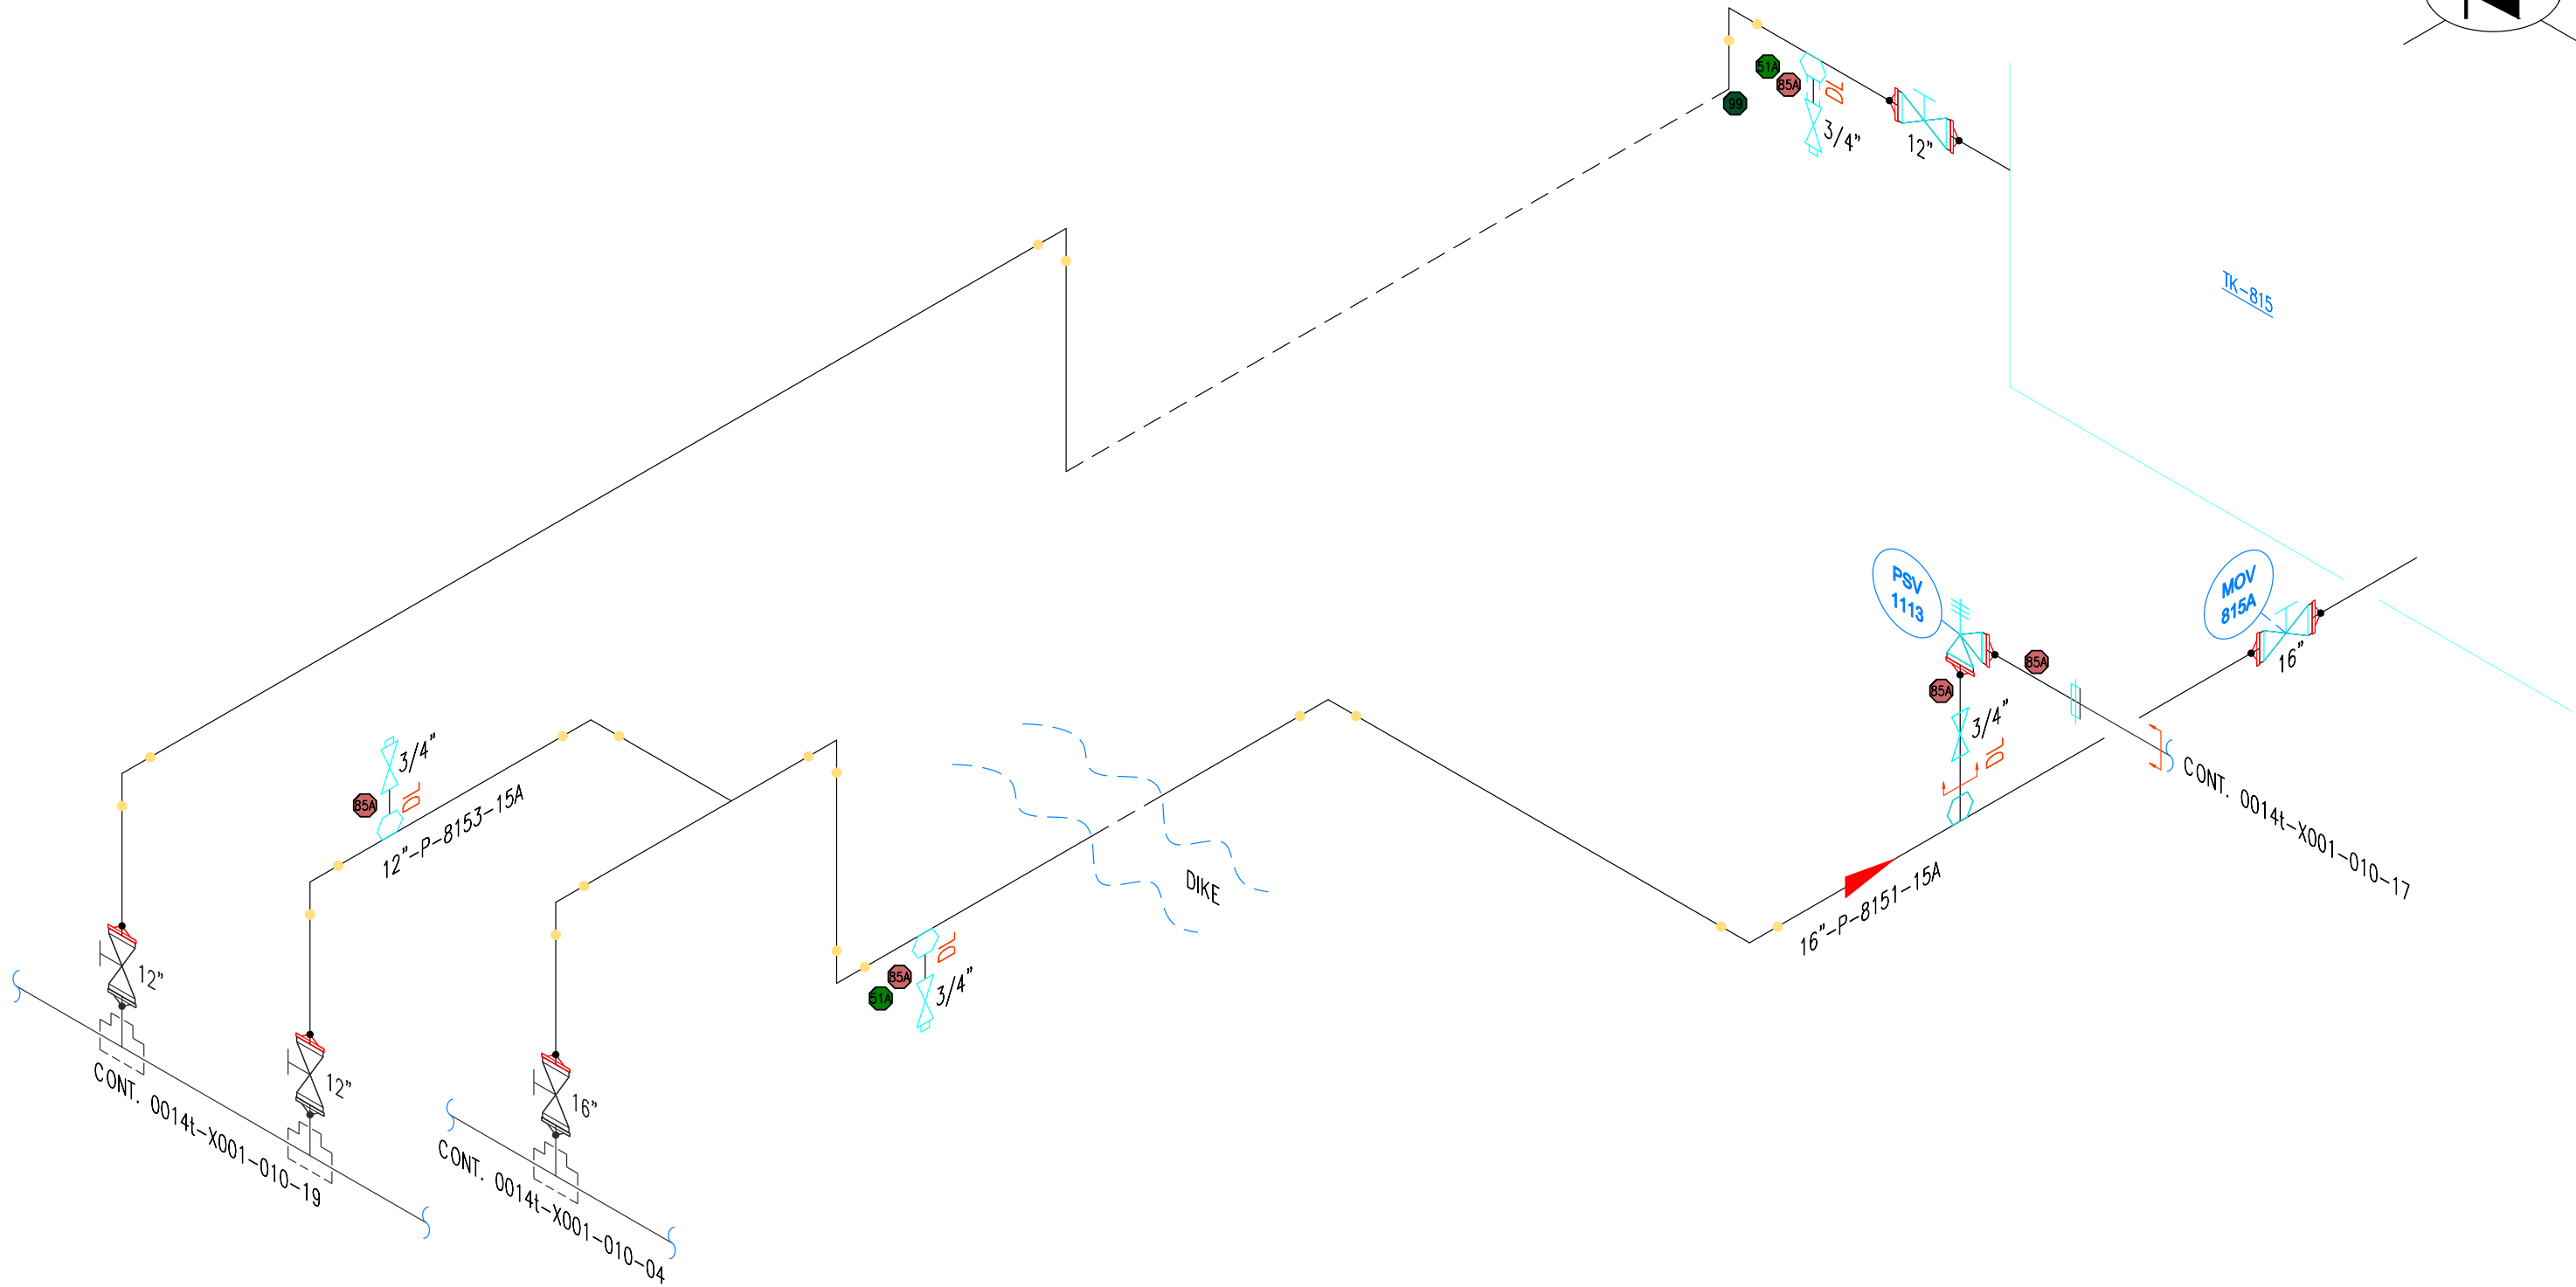


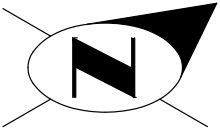

REFERENCES		CML LEGEND	NOTES	REVISIONS	0 ISSUED FOR FEAS PROJECT 05/23/25	 Chevron Pasadena Refinery	MATERIAL		INSPECTION PIPING ISOMETRIC							
P&ID	LEGACY ISO															
14t-11-F14501	14-CRUDE-L001 PG. 2 OF 15	☐ RT1 0° SHOT	1. API PIPE CLASS -													
-	14-CRUDE-L001 PG. 11 OF 15	☐ RT2 0° AND 90° SHOT	2. CVX PIPE SPEC -													
-	14-CRUDE-L002 PG. 9 OF 13	☐ UT1 SINGLE POINT UT	3. OP TEMP. -													
-	14-CRUDE-L004 PG. 9 OF 10	☐ UT4 4 POINT UT	4. FROM -													
-	-	☐ UTS SCAN UT (100%)	5. TO -													
-	-	☐ UTG GRID UT	6. MISC. -													
-	-	☐ AUT AUTOMATED UT	* SULFIDATION POINT													
-	-	+ ADDITIONAL INSPECTION CML														
							DR. BY:	PART	DATE:	05/23/25						
							CHK. BY:	PART	DATE:	-	INSULATED? PWHT?	NO NO	PLANT NUMBER SYSTEM NUMBER CIRCUIT NUMBER SHEET NUMBER REV. 0014t - X001 - 010 - 18 0			