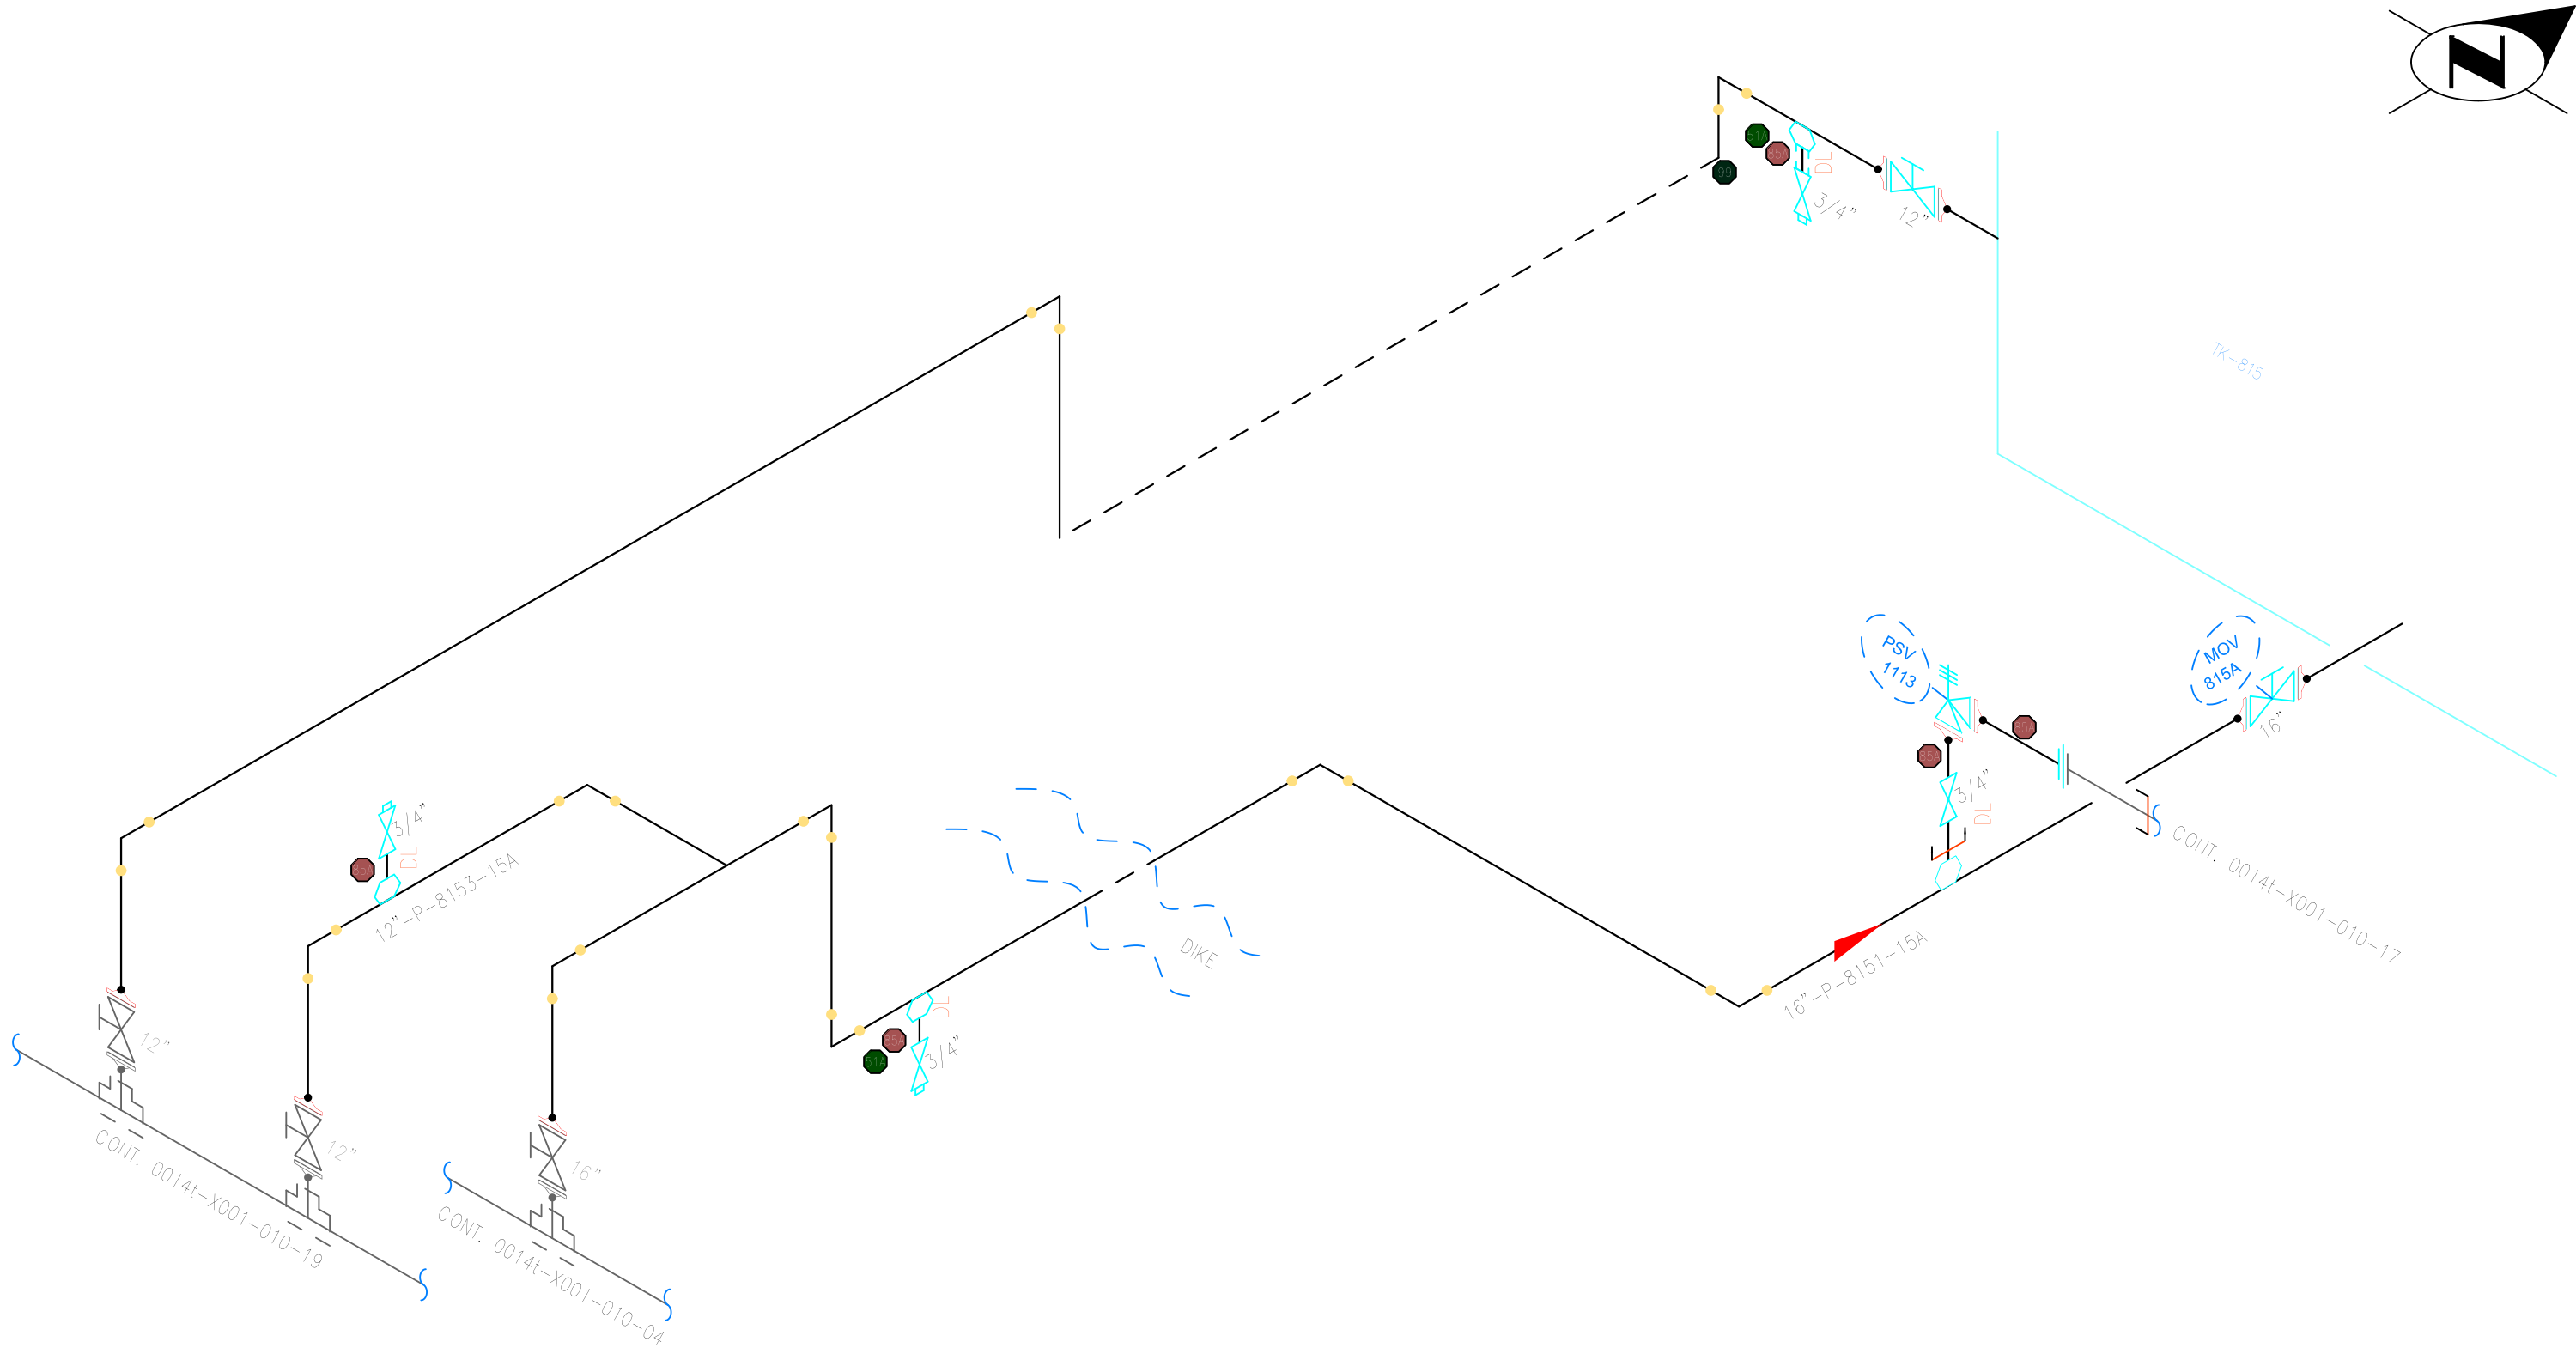


REFERENCES		CML LEGEND		NOTES		0 ISSUED FOR FEAS PROJECT		Chevron Chevron Pasadena Refinery		MATERIAL		INSPECTION PIPING ISOMETRIC												
P&ID	LEGACY ISO	RT1	0° SHOT	1. API PIPE CLASS -																				
14t-11-F14501	14-CRUDE-L001 PG. 2 OF 15	RT2	0° AND 90° SHOT	2. CVX PIPE SPEC -	REVISIONS		05/23/25																	
-	14-CRUDE-L001 PG. 11 OF 15	UT1	SINGLE POINT UT	3. OP TEMP. -																				
-	14-CRUDE-L002 PG. 9 OF 13	UT4	4 POINT UT	4. FROM -																				
-	14-CRUDE-L004 PG. 9 OF 10	UTS	SCAN UT (100%%%)	5. TO -																				
-	-	UTG	GRID UT	6. MISC. -																				
-	-	AUT	AUTOMATED UT																					
-	-	+	ADDITIONAL INSPECTION CML	*SULFIDATION POINT																				
								DR. BY: PART		DATE: 05/23/25			PLANT NUMBER		SYSTEM NUMBER		CIRCUIT NUMBER		SHEET NUMBER		REV.			
								CHK. BY: PART		DATE: -	INSULATED? NO				0014t		- X001		- 010		- 18		0	
											PWHT? NO													