
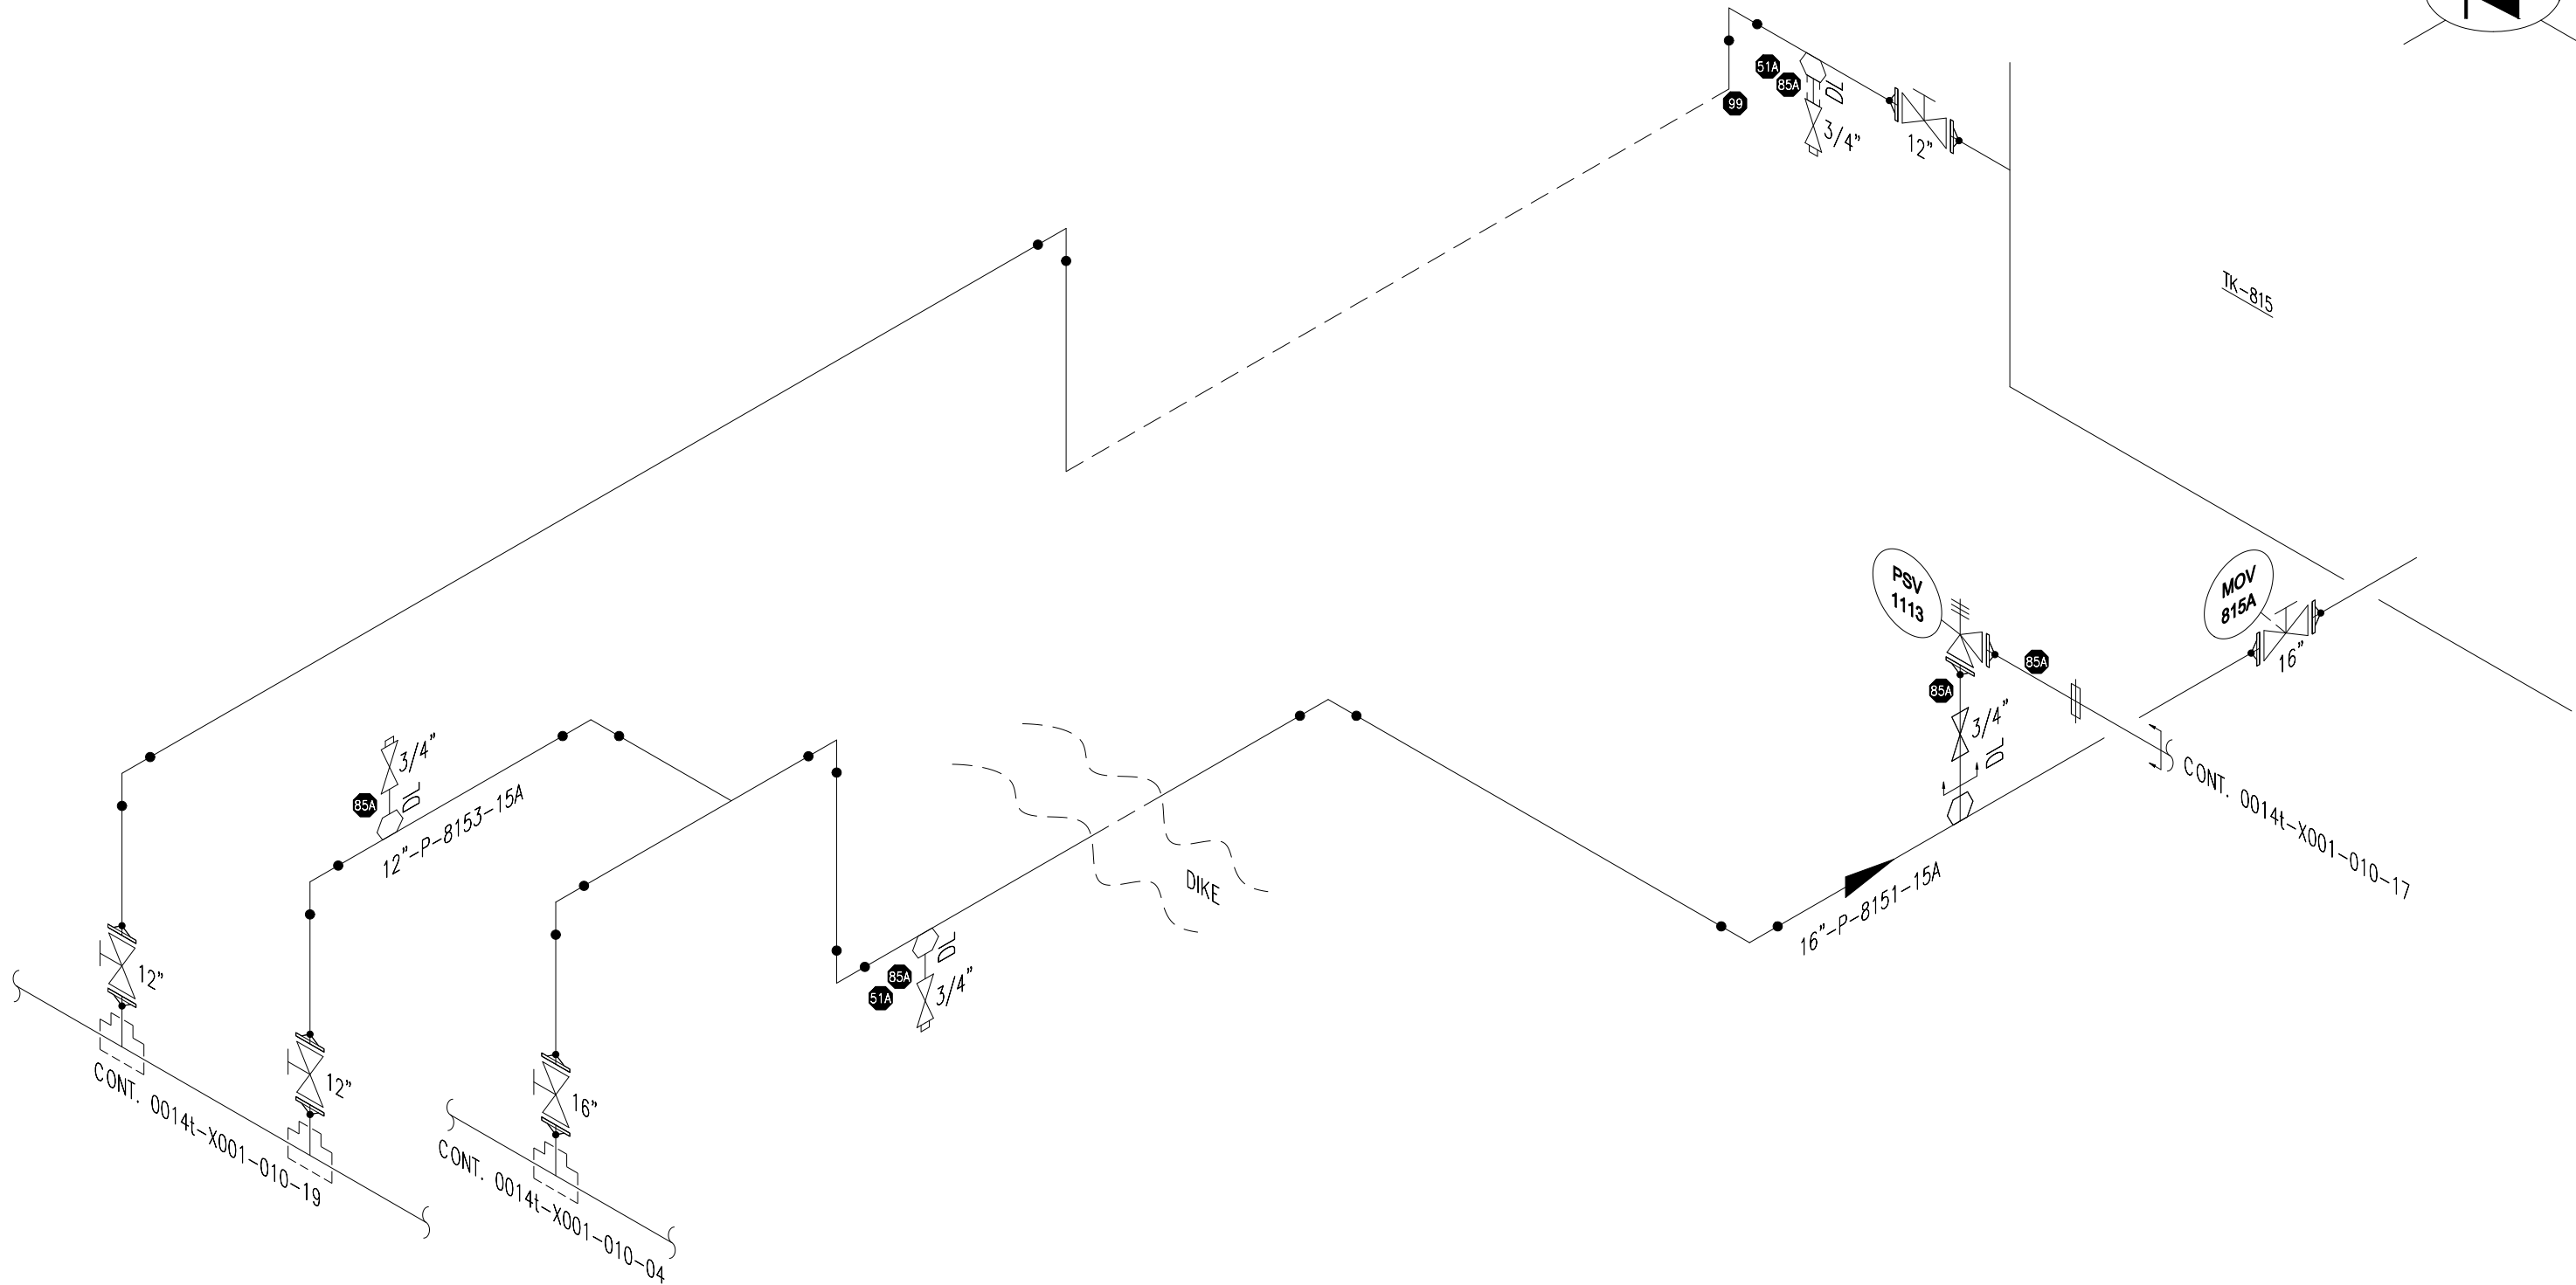


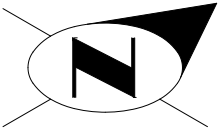

REFERENCES		CML LEGEND	NOTES	ISSUED FOR FEAS PROJECT		MATERIAL		INSPECTION PIPING ISOMETRIC				
P&ID	LEGACY ISO											
14t-11-F14501	14-CRUDE-L001 PG. 2 OF 15	☐ RT1 0° SHOT	1. API PIPE CLASS -	05/23/25		-	-					
-	14-CRUDE-L001 PG. 11 OF 15	☐ RT2 0° AND 90° SHOT	2. CVX PIPE SPEC -									
-	14-CRUDE-L002 PG. 9 OF 13	☐ UT1 SINGLE POINT UT	3. OP TEMP. -									
-	14-CRUDE-L004 PG. 9 OF 10	☐ UT4 4 POINT UT	4. FROM -									
-	-	☐ UT5 SCAN UT (100%)	5. TO -									
-	-	☐ UT6 GRID UT	6. MISC. -	-	PART	DATE:	PWHT?					
-	-	☐ AUT AUTOMATED UT	* SULFIDATION POINT									
-	-	☐ + ADDITIONAL INSPECTION CML						PLANT NUMBER	SYSTEM NUMBER	CIRCUIT NUMBER	SHEET NUMBER	REV.
								0014t	- X001	- 010	- 18	0