
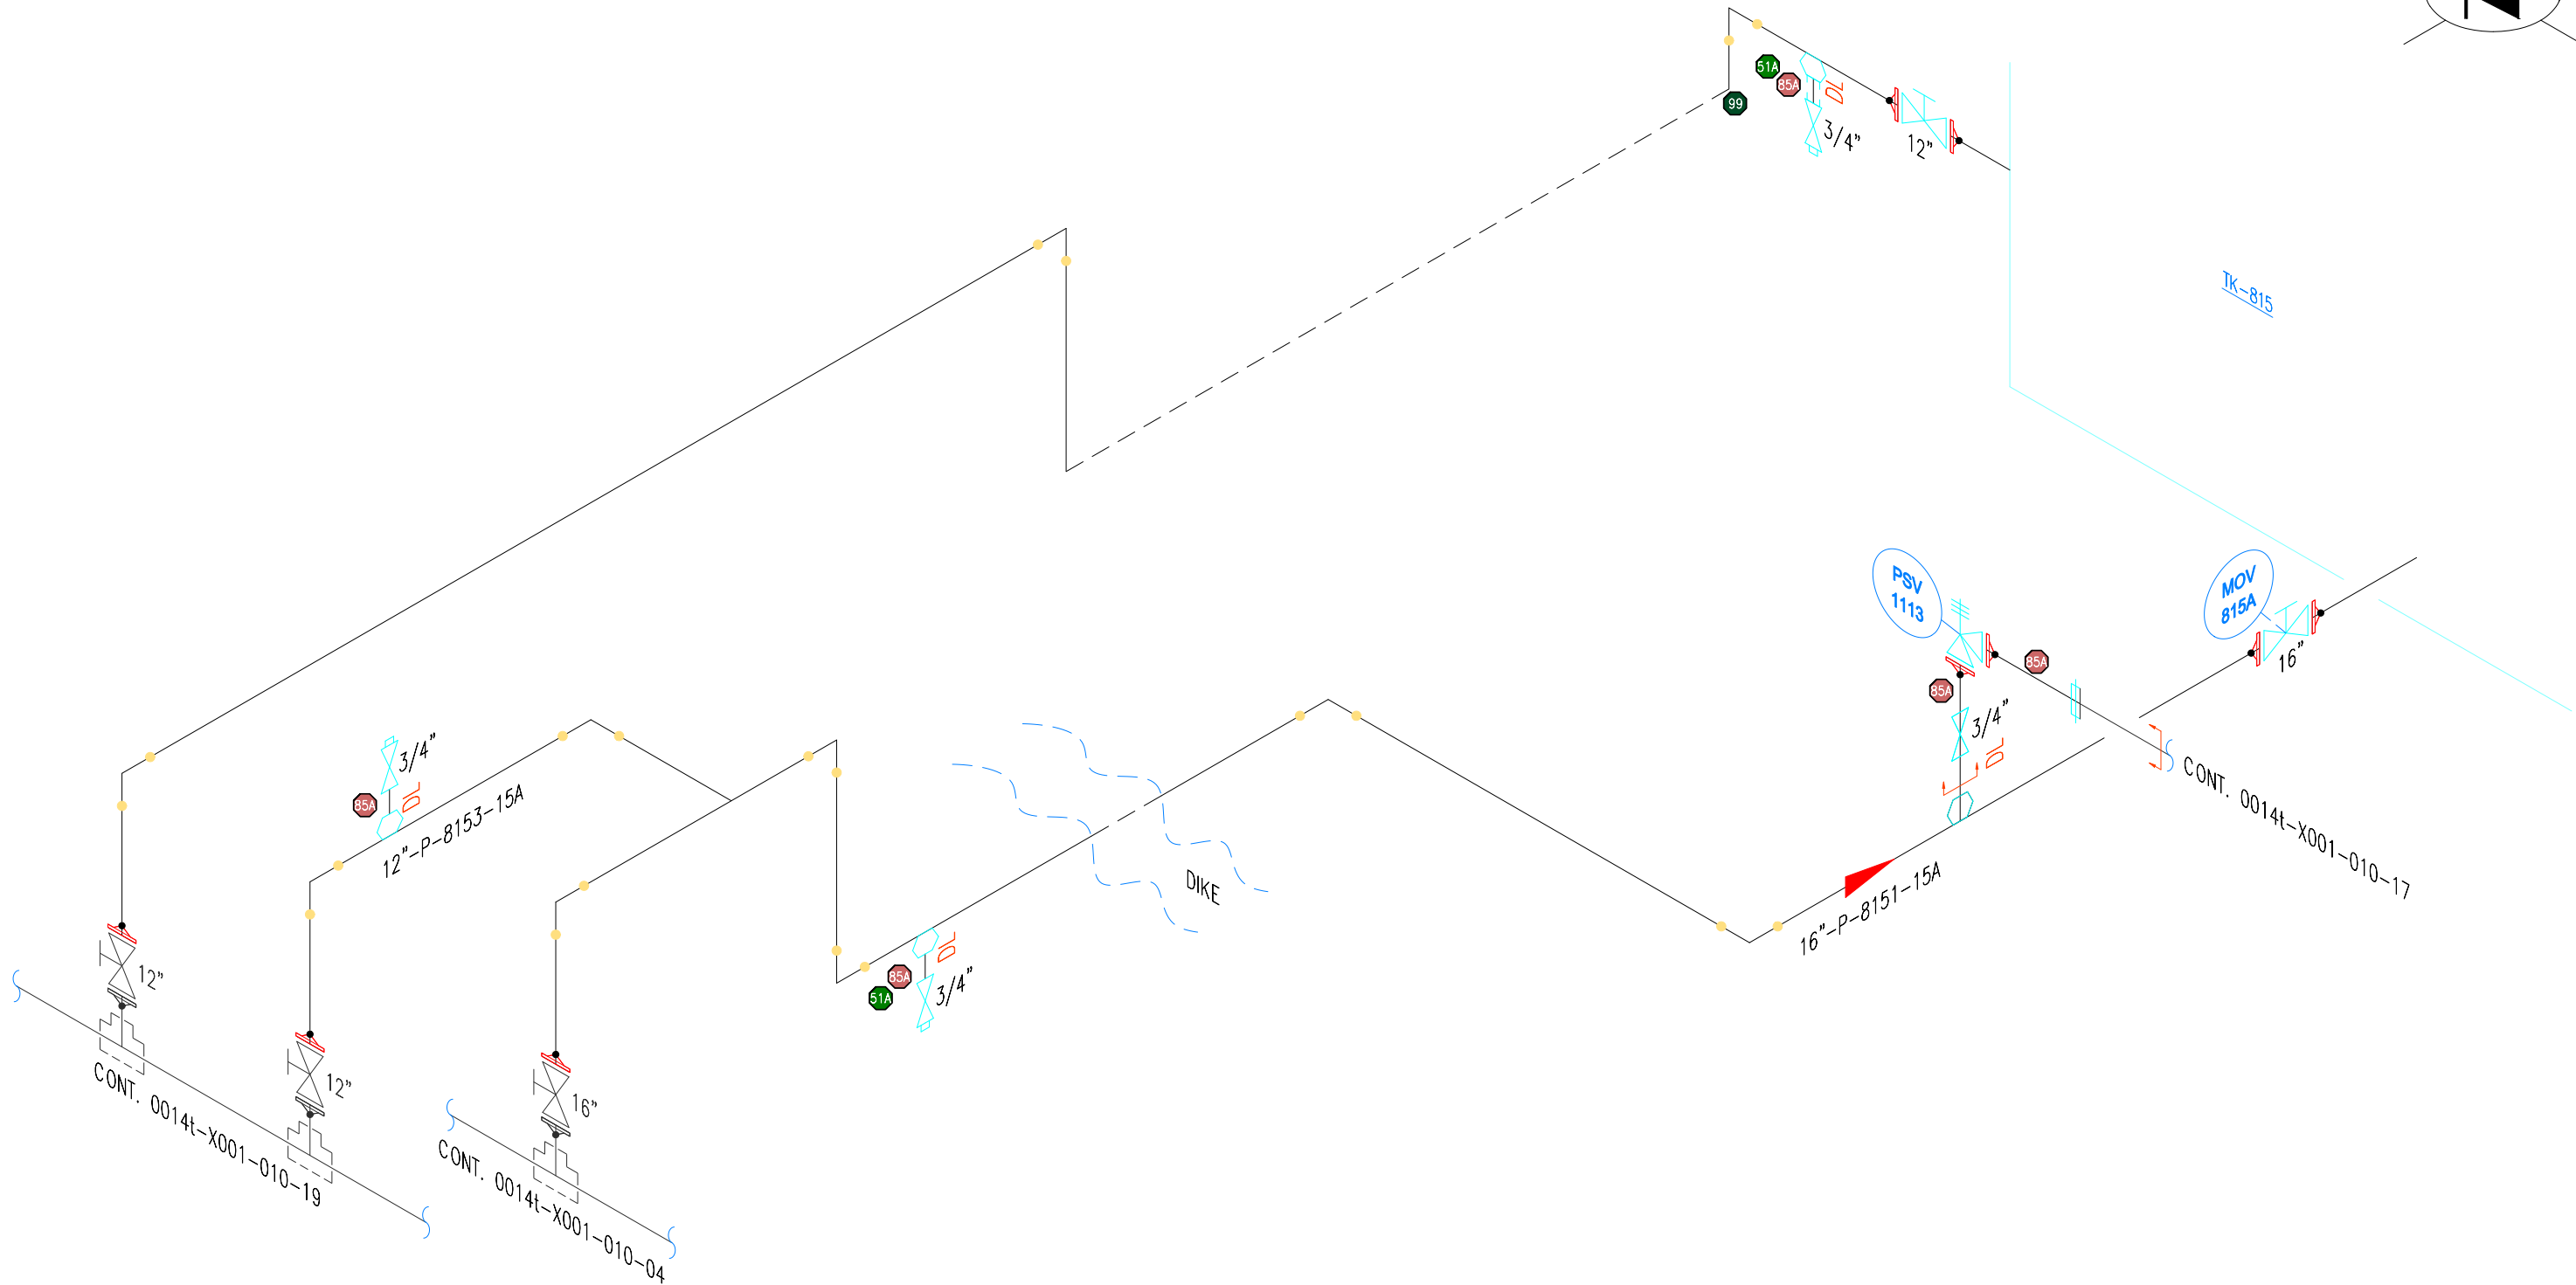


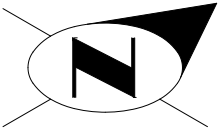

REFERENCES		CML LEGEND		NOTES		ISSUED FOR FEAS PROJECT		Chevron Pasadena Refinery		MATERIAL		INSPECTION PIPING ISOMETRIC								
P&ID	LEGACY ISO	RT1	0° SHOT	1. API PIPE CLASS -																
14t-11-F14501	14-CRUDE-L001 PG. 2 OF 15	RT2	0° AND 90° SHOT	2. CVX PIPE SPEC -	REVISIONS	05/23/25				-	-									
-	14-CRUDE-L001 PG. 11 OF 15	UT1	SINGLE POINT UT	3. OP TEMP. -						-	-									
-	14-CRUDE-L002 PG. 9 OF 13	UT4	4 POINT UT	4. FROM -						-	-									
-	14-CRUDE-L004 PG. 9 OF 10	UTS	SCAN UT (100%)	5. TO -						-	-									
-	-	UTG	GRID UT	6. MISC. -						-	-									
-	-	AUT	AUTOMATED UT	* SULFIDATION POINT						-	-									
-	-	+ ADDITIONAL INSPECTION CML						DR. BY:	PART	DATE:	05/23/25	INSULATED? NO		PLANT NUMBER			SYSTEM NUMBER	CIRCUIT NUMBER	SHEET NUMBER	REV.
-	-							CHK. BY:	PART	DATE:	-	PWHT? NO		0014t -			X001 -	010 -	18	0